



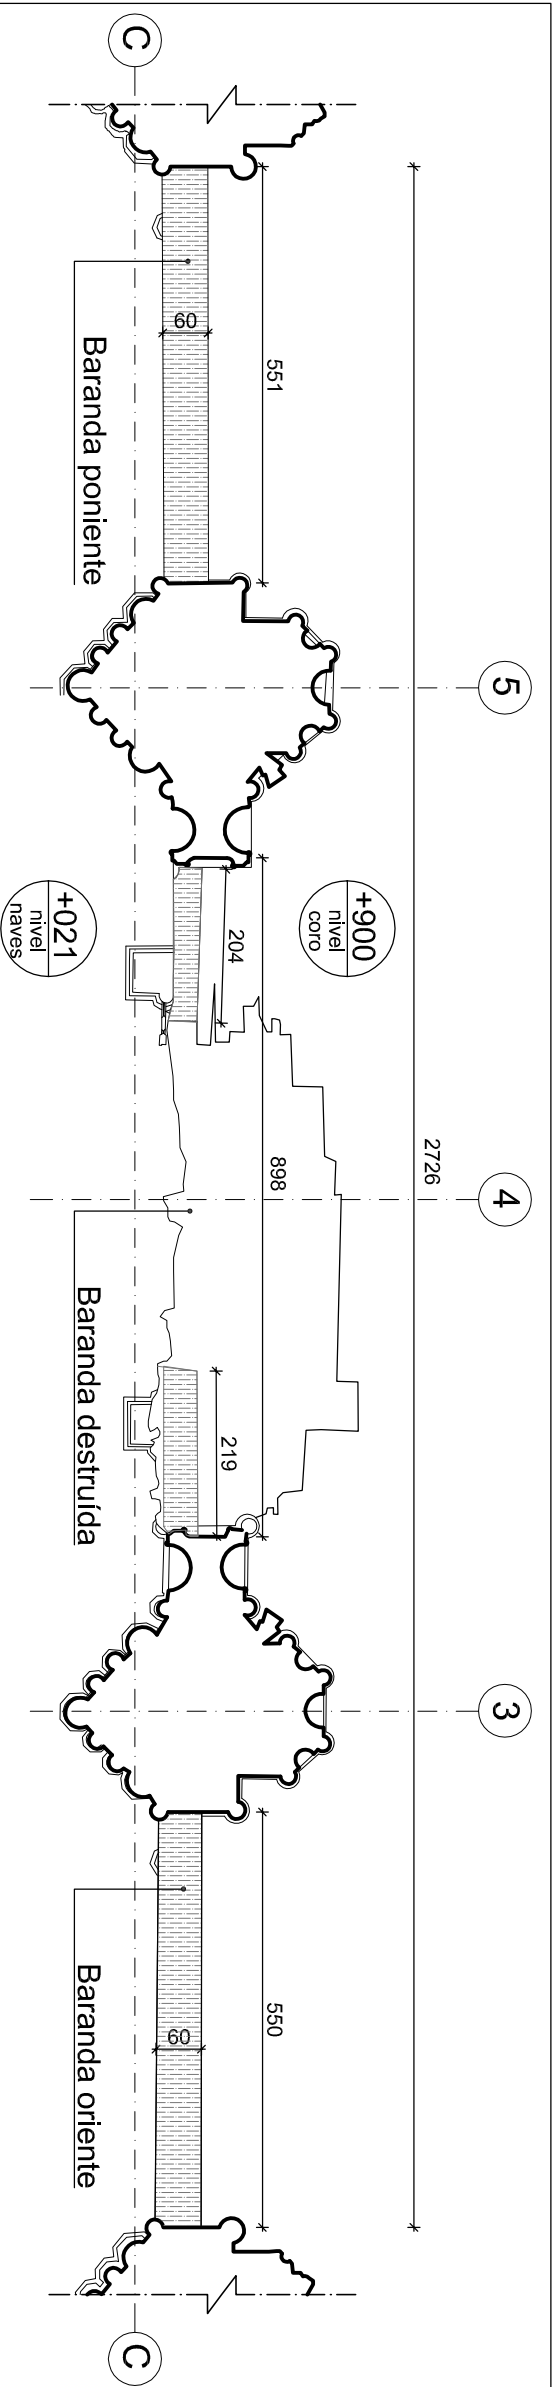


PLANTA GENERAL BARANDA CORO

Esc. 1/100

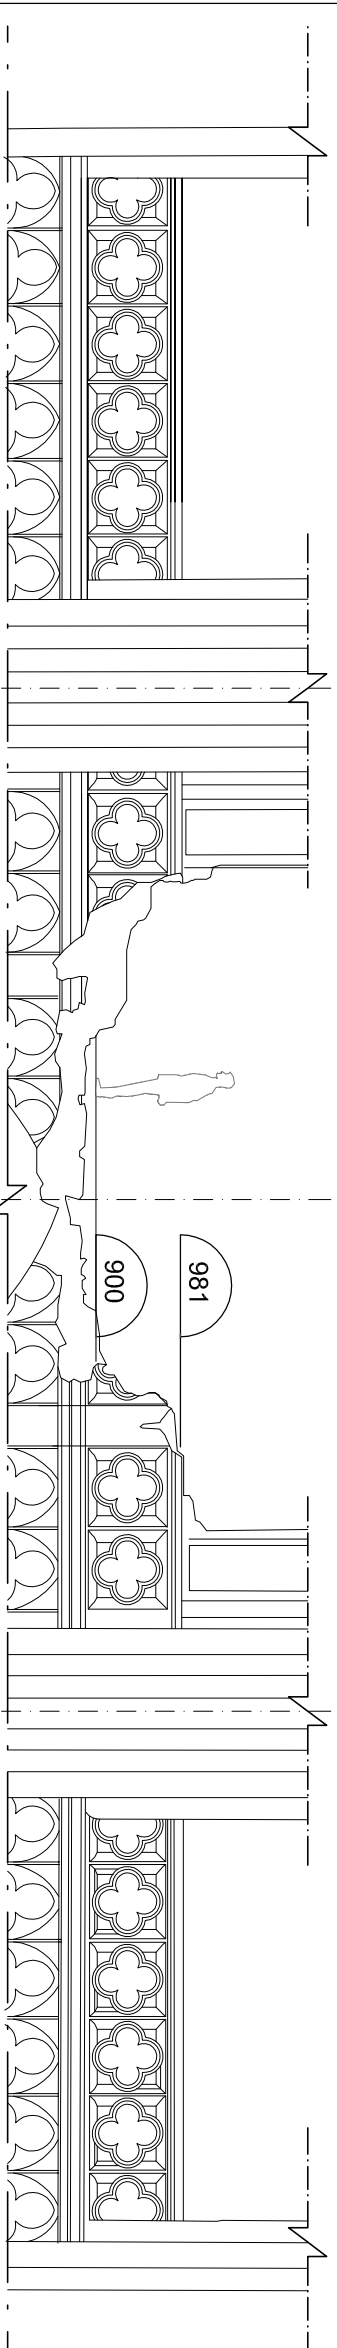

ELEVACIÓN GENERAL BARANDA CORO

Esc. 1/100

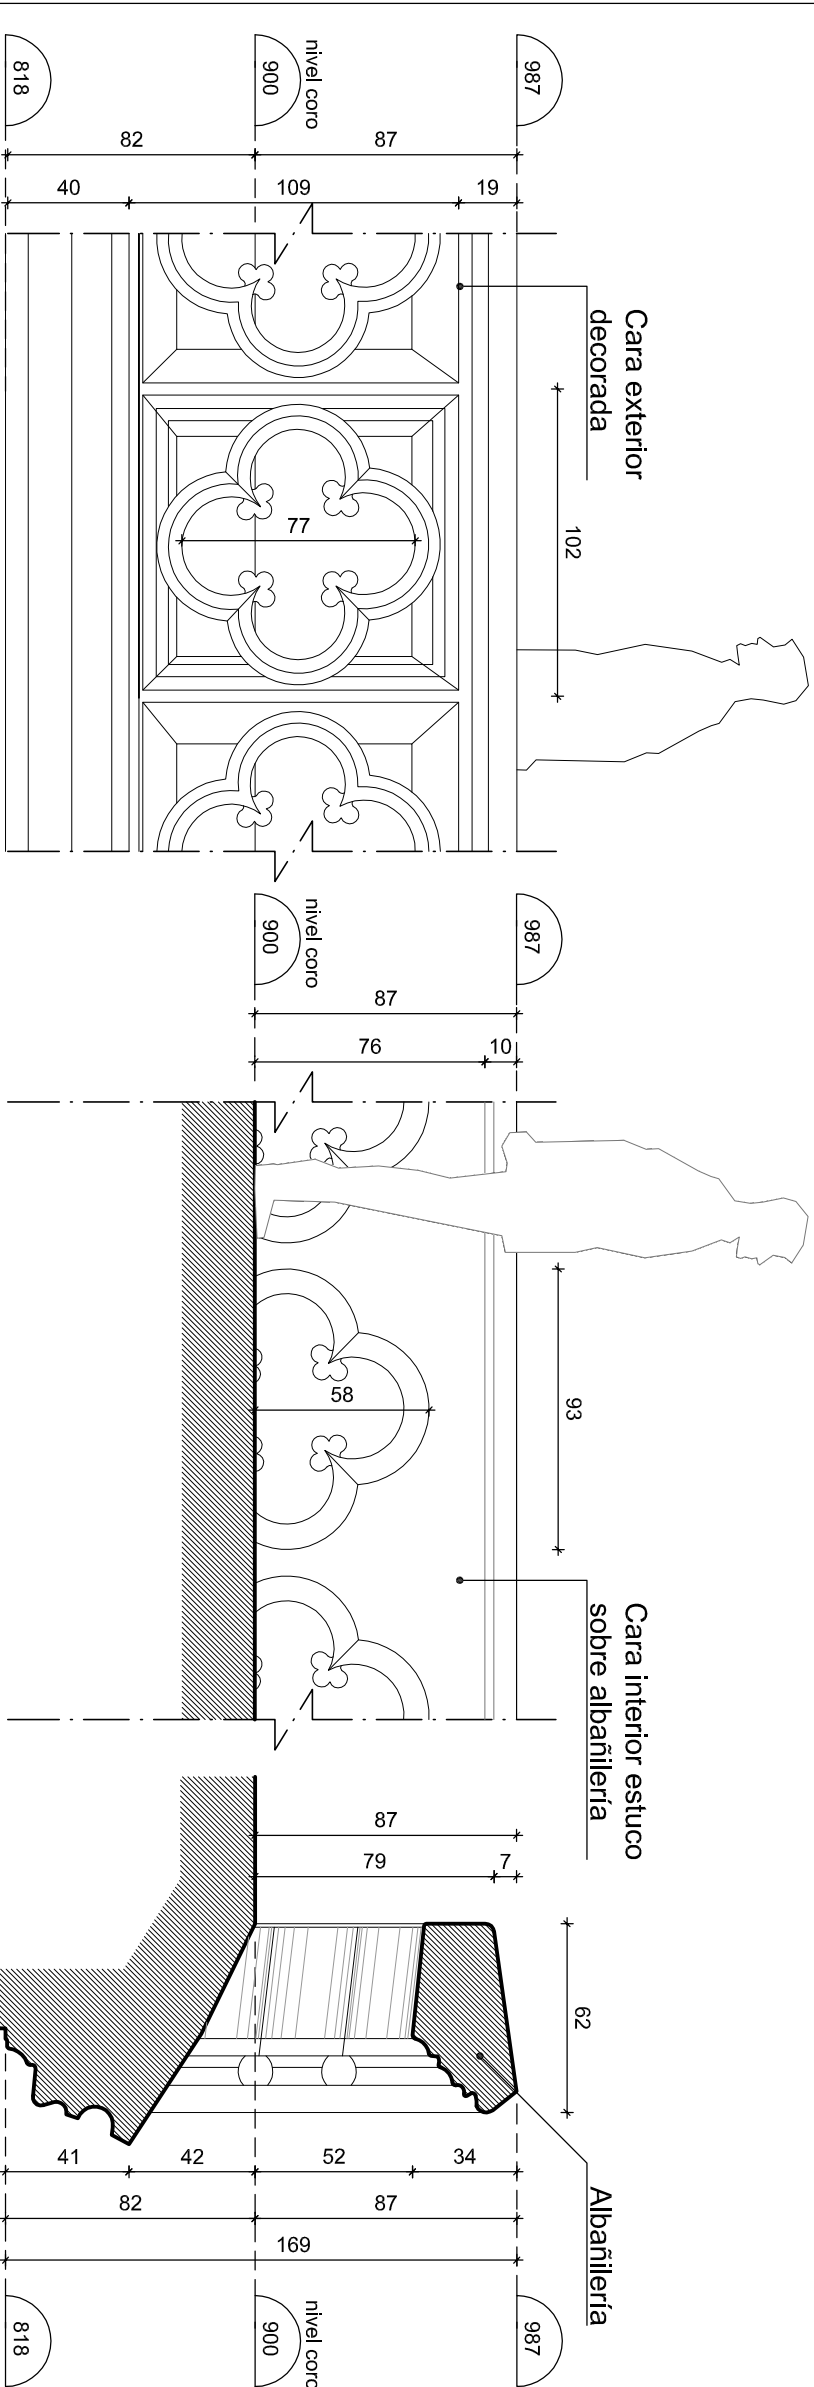

ELEVACIÓN TIPO NAVE


Esc. 1/25

ELEVACIÓN TIPO CORO

Esc. 1/25


SECCIÓN A

Esc. 1/25

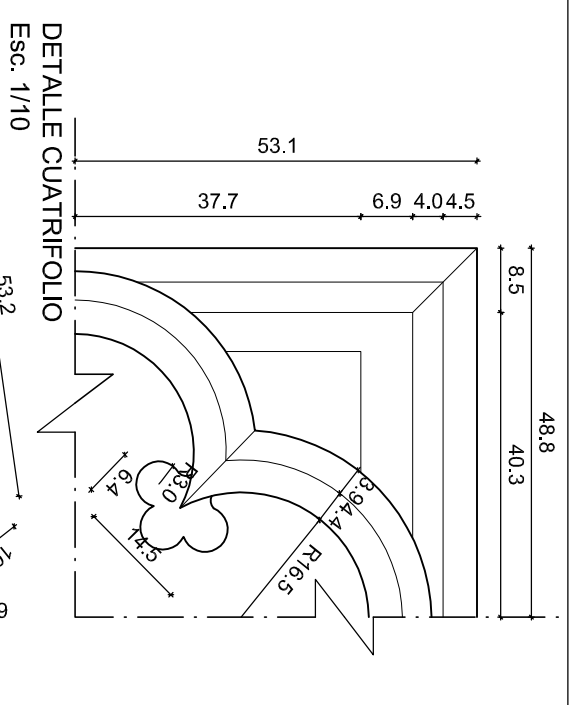


DETALLE CUATRIFOLIO

Esc. 1/10

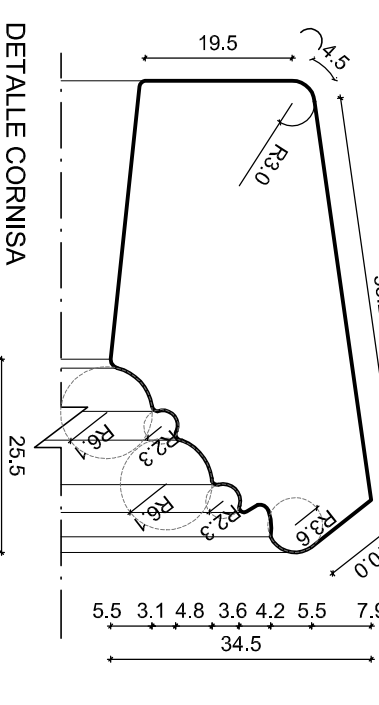

DETALLE CORNISA

Esc. 1/10

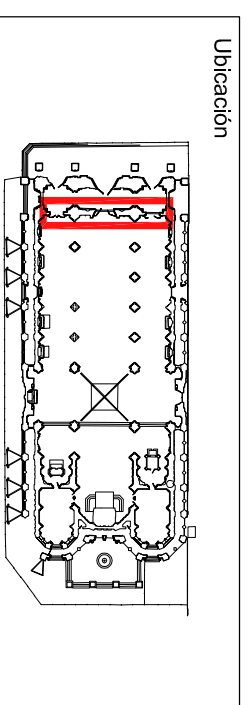

Ubicación		PROYECTO	
		Arqto. Dino Bozzi F. TÁNDEM Limitada contacto@tandemlimitada.cl	
DIRECCIÓN DE ARQUITECTURA DIRECCIÓN REGIONAL METROPOLITANA		PROYECTO: REPARACIÓN PARCIAL BASÍLICA DEL SALVADOR STIGO	

BASÍLICA DEL SALVADOR		ES	
Huérfanos 1796 - Santiago		Ba-01	
Región Metropolitana			

DETALLE BARANDA CORO				varias	Ago.13
TD	TD	LEV	DET	-	A
Emisor	Proyecto	Fase	Tipo	Zona	Índice
Dibuj: RM	Control: VI	Archivo de ref.: TD_1212_LEV_ES_Ba01g			