

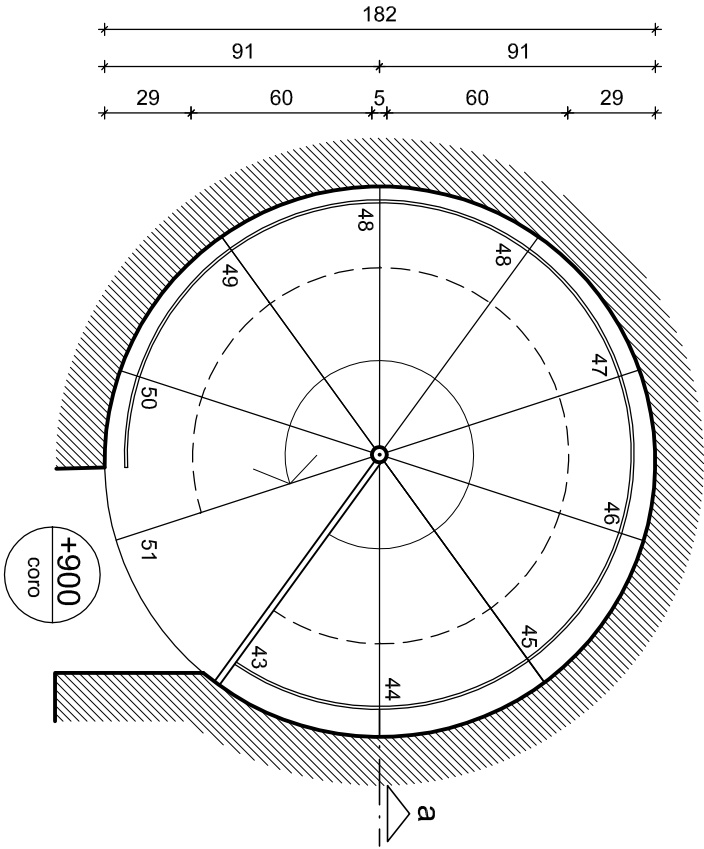
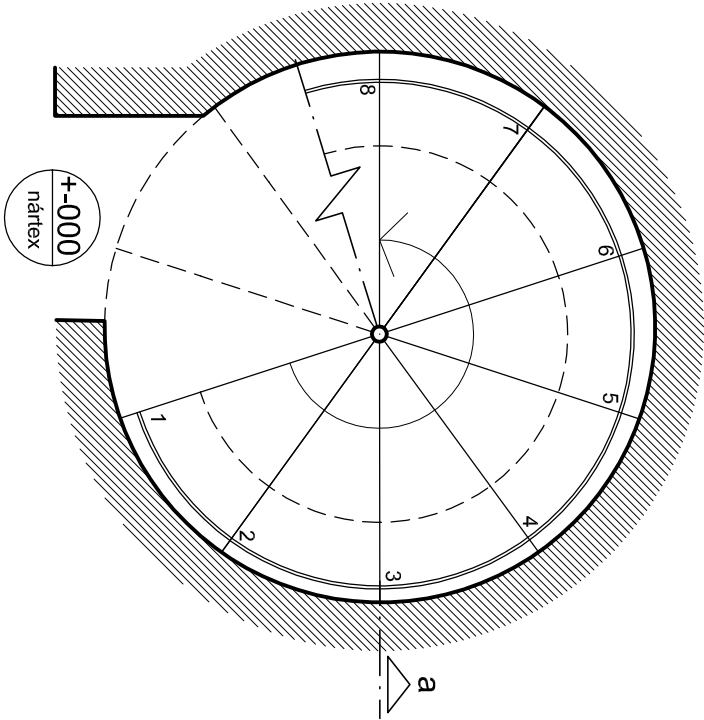


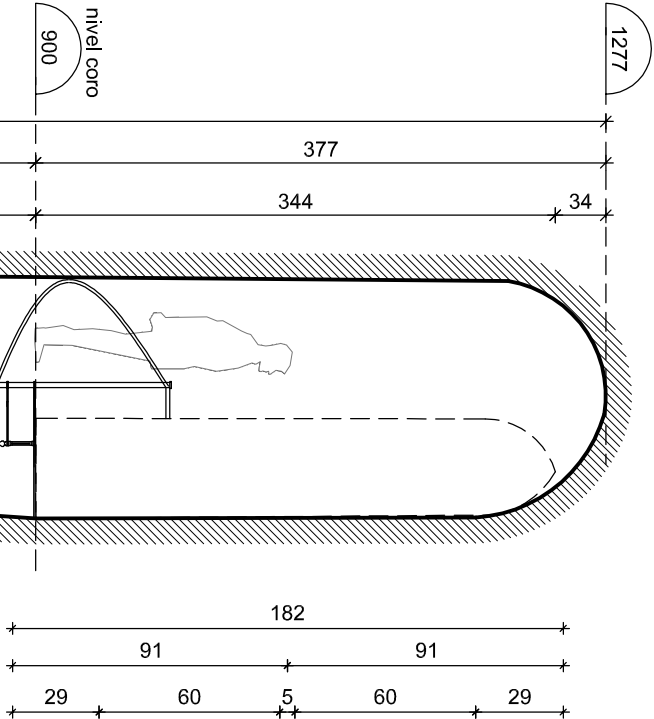


PLANTA NIVEL NÁRTEX
Esc. 1/25



PLANTA NIVEL CORO
Esc. 1/25

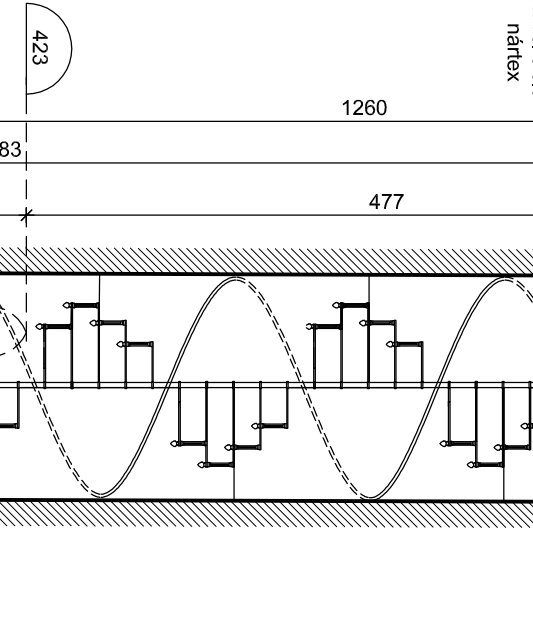


DETALLE HUELLO TIPO
Esc. 1/10

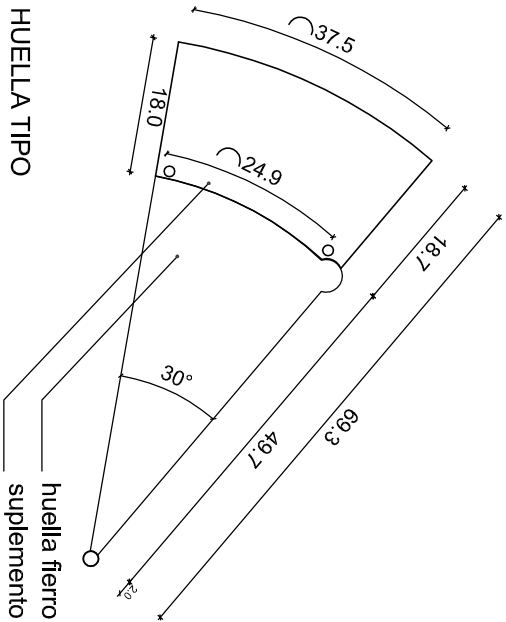

DETALLE APOYO HUELLO TIPO
Esc. 1/5

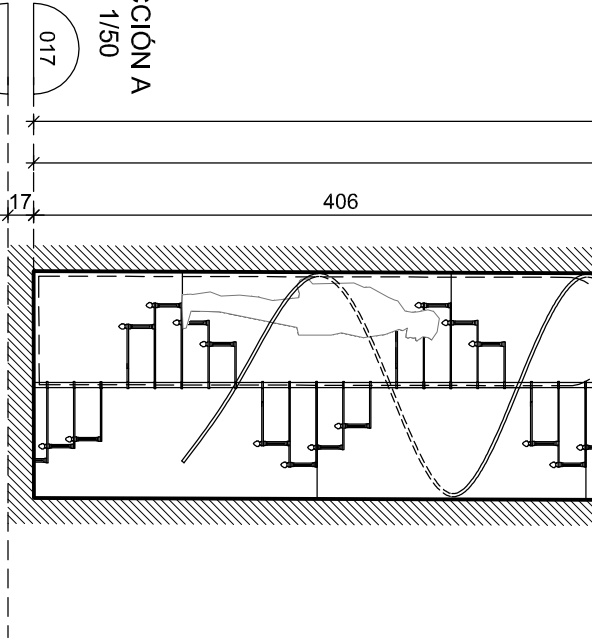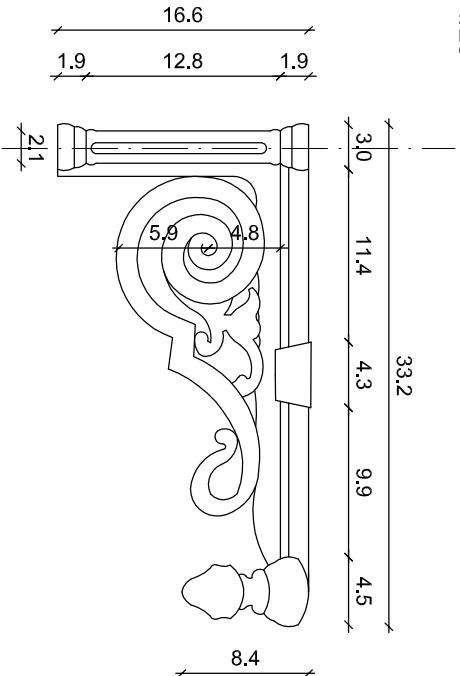

DETALLE CONTRAHUELLO
Esc. 1/5

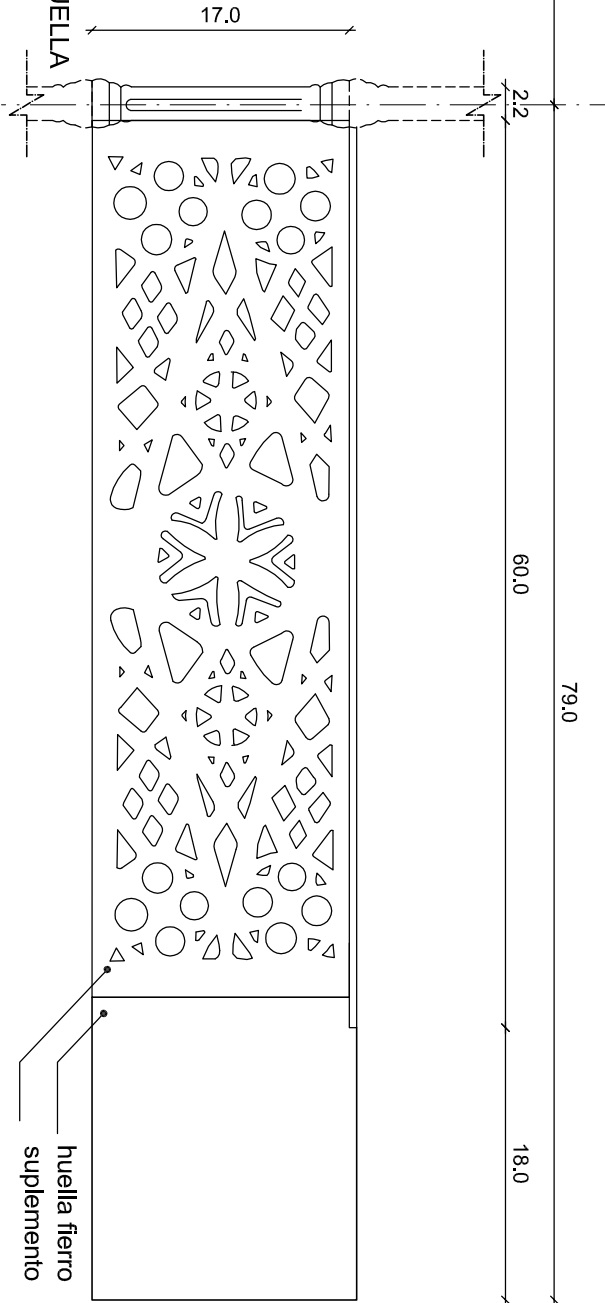

Detalle contrahuella



Detalle baranda



Detalle suplementos




Detalle huellas



Detalle pasamanos



Detalle baranda

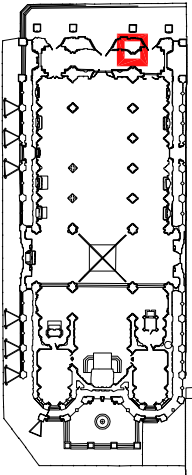

Ubicación



Arqto. Dino Bozzi F.
TÁNDEM Limitada
contacto@tandemlimitada.cl

PROYECTO

DIRECCIÓN DE ARQUITECTURA
DIRECCIÓN REGIONAL METROPOLITANA

PROYECTO: REPARACIÓN PARCIAL BASÍLICA DEL
SALVADOR STIGO

BASÍLICA DEL SALVADOR
Huérfanos 1796 - Santiago
Región Metropolitana





ES
Esc-1

LEVANTAMIENTO ESCALERA
nártex hacia coro

varias
Ago. 13
Escala
Fecha

TD TD 1305 LEV DET - A

Emisor Proyecto Fase Tipo Zona Índice
Dibuj: RL Control: VI Archivo de ref.: TD_1212_LEV_ES_Esc-01.dwg

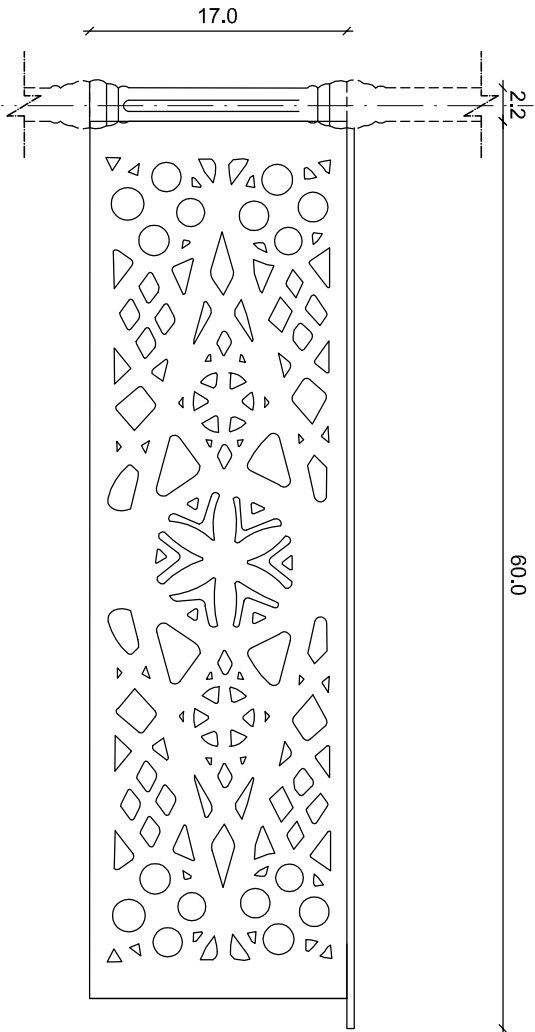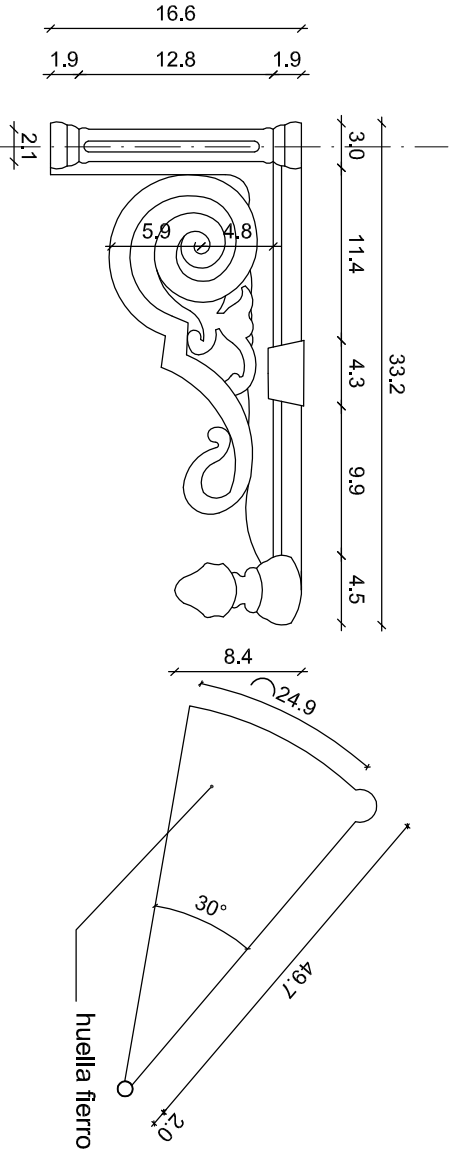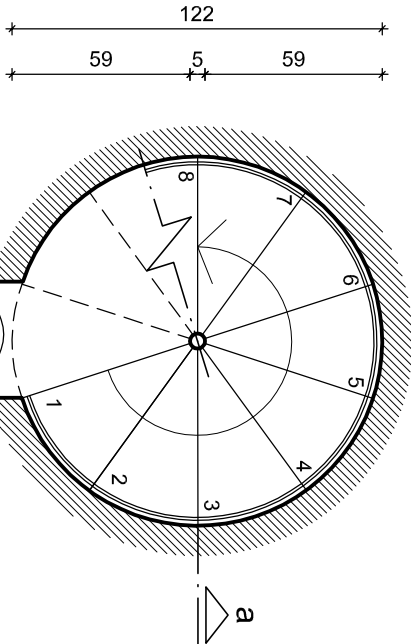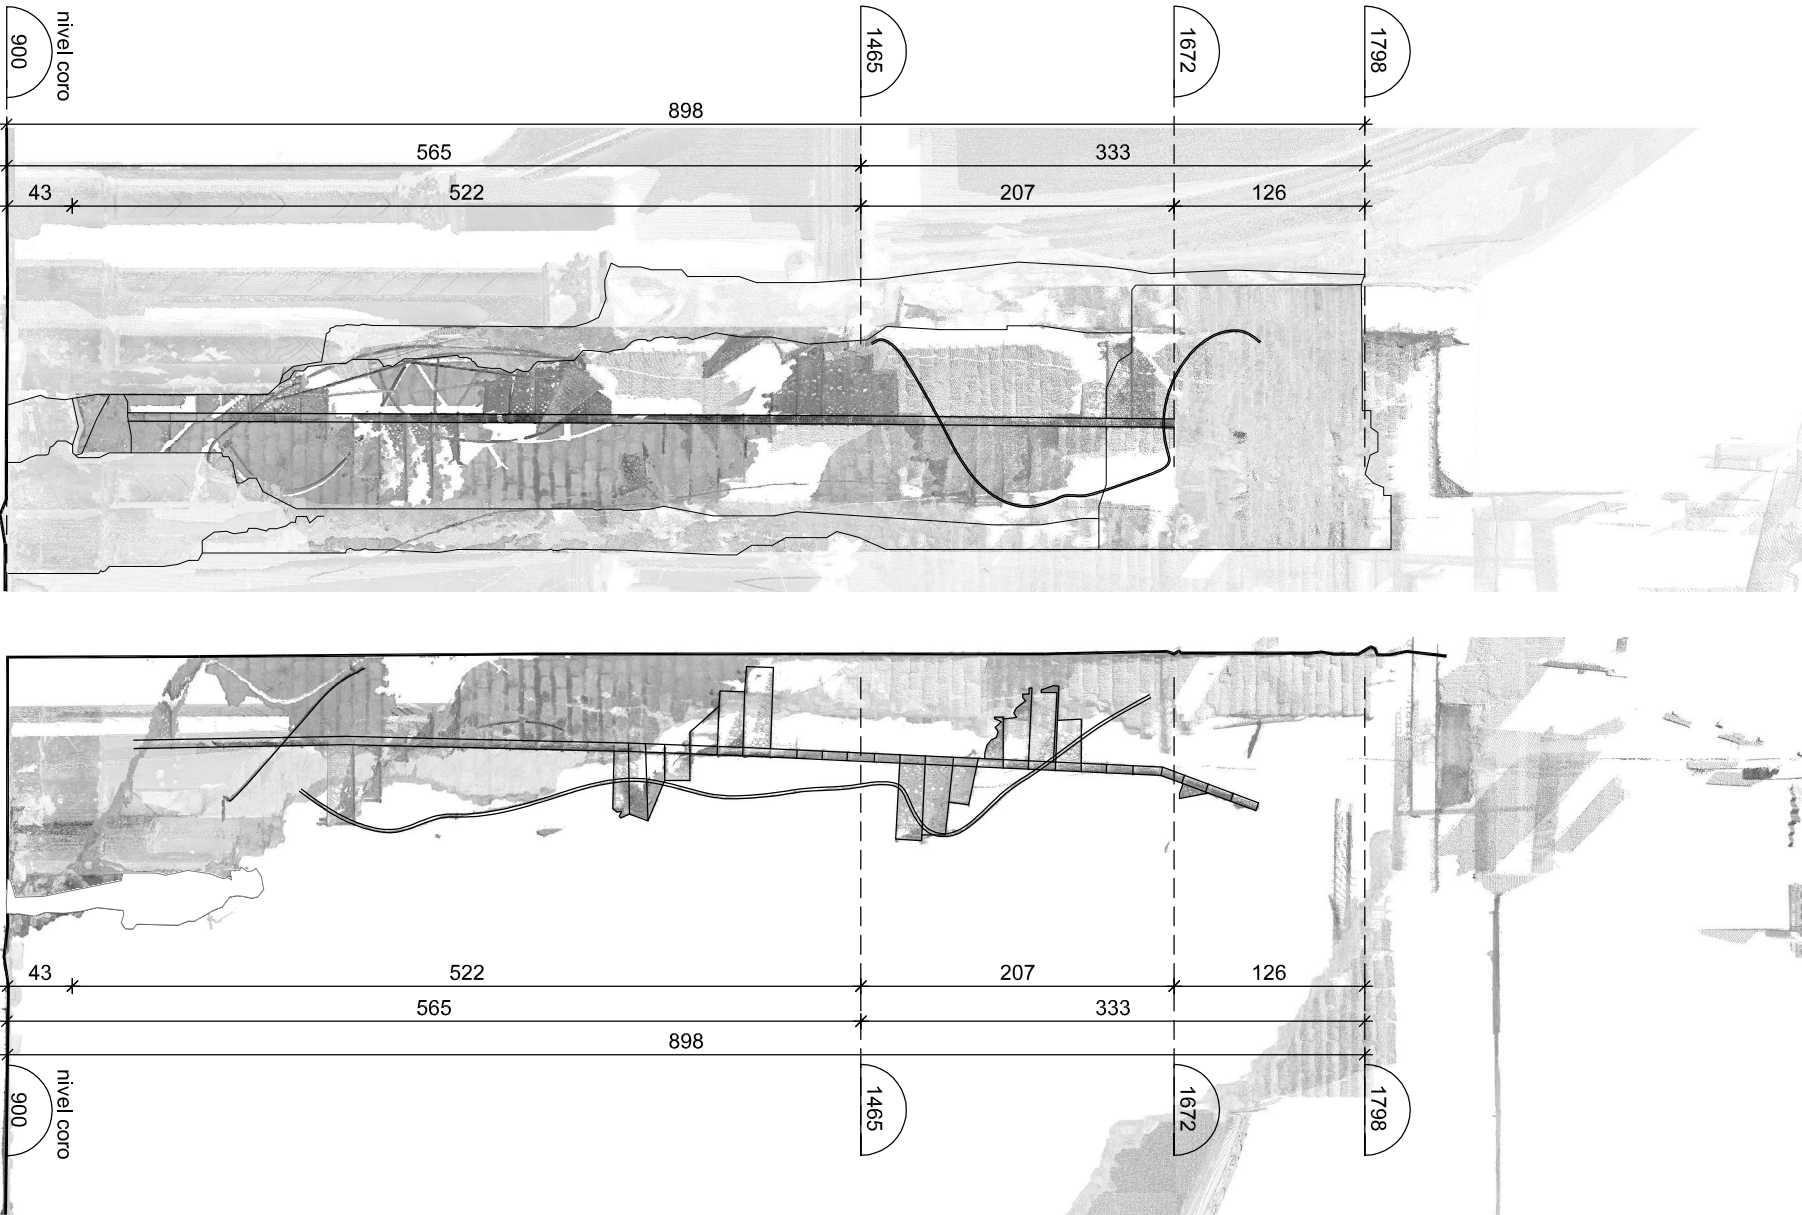

Ubicación						
				PROYECTO		
DIRECCIÓN DE ARQUITECTURA DIRECCIÓN REGIONAL METROPOLITANA				Arqto. Dino Bozzi F. TÁNDEM Limitada contacto@tandemlimitada.cl		
PROYECTO: REPARACIÓN PARCIAL BASÍLICA DEL SALVADOR STGO						
BASÍLICA DEL SALVADOR				ES		
Huérfanos 1796 - Santiago Región Metropolitana				Esc-2		
LEVANTAMIENTO ESCALERA coro hacia campanario				1/25	Ago. 13	
TD	TD 1305	LEV	DET	-	A	
Emisor	Proyecto	Fase	Tipo	Zona	Índice	
Dibujó: RL				Control : VI		
Archivo de ref.: TD_1212_LEV_ES_Esc-01.dwg						