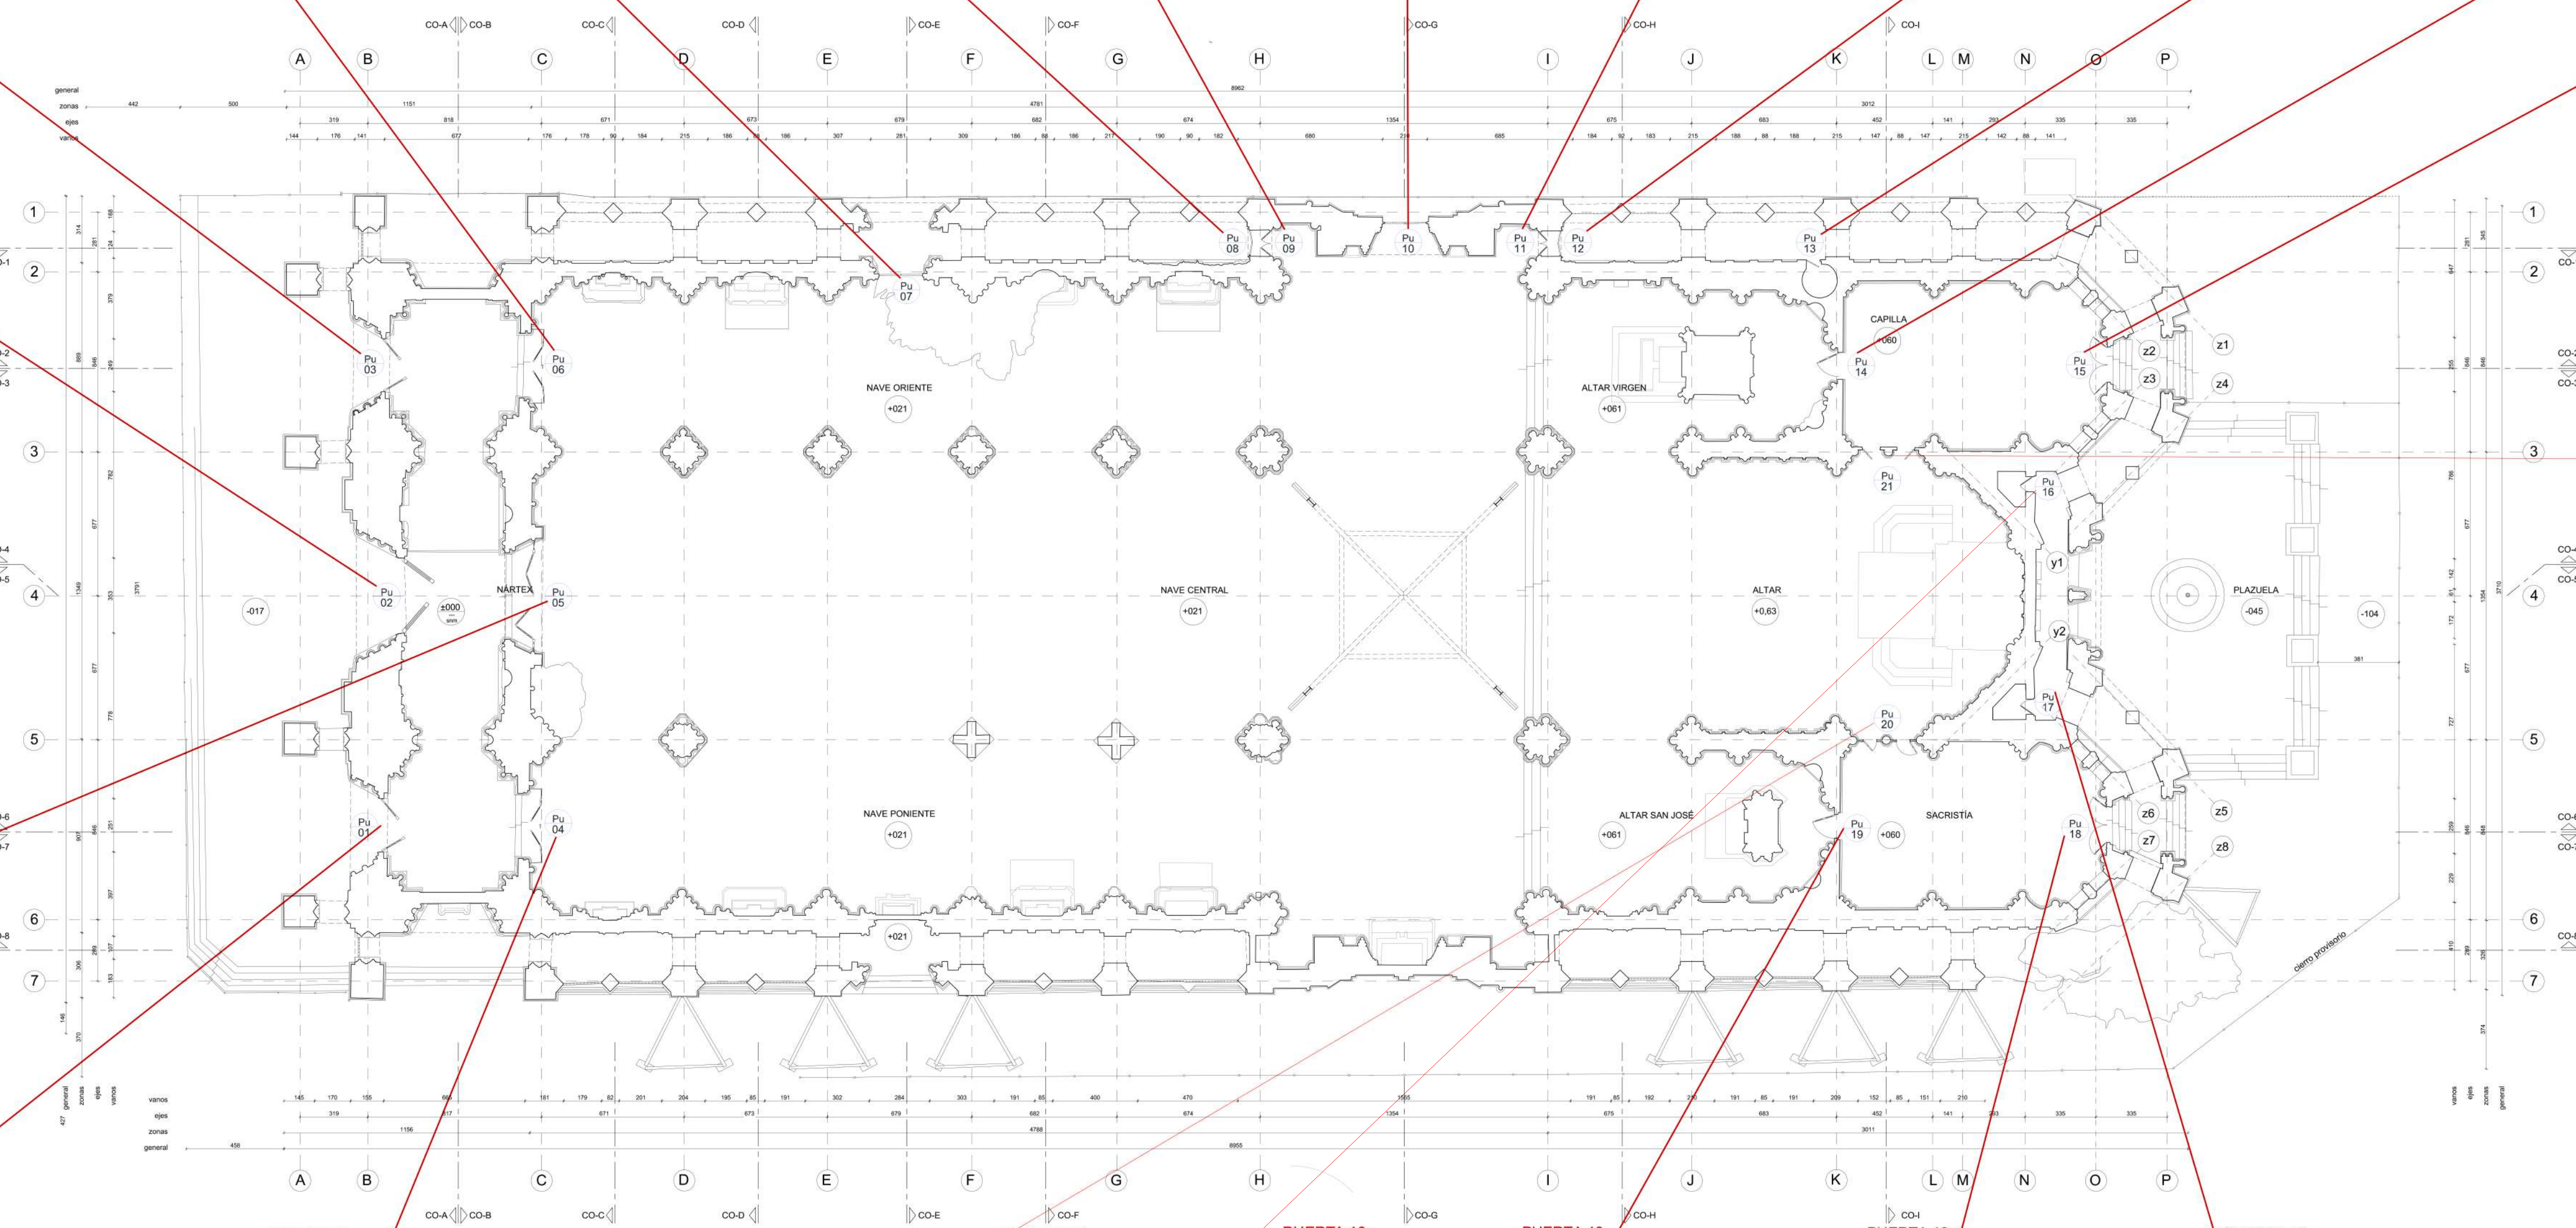
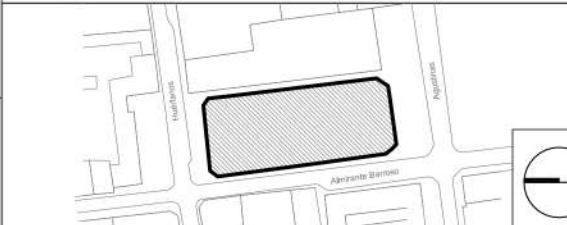


[illegible]

OBSERVACIONES			
 Dirección de Arquitectura Ministerio de Obras Públicas Gobierno de Chile		DIRECCIÓN DE ARQUITECTURA DIRECCIÓN REGIONAL METROPOLITANA	
REGIÓN: METROPOLITANA PROVINCIA: SANTIAGO COMUNA: SANTIAGO PROYECTO		PROYECTO: REPARACIÓN PARCIAL BASÍLICA DEL SALVADOR STGO PLANO: DISEÑO CONCEPTUAL OBRAS EMERGENCIA PROPIETARIO: ARZOBISPADO DE SANTIAGO JEFE U. DE DISEÑO	
Argto. Dino Bozzi F. - Tándem			
DIBUJO V.I.G.	REVISIÓN D.B.F	DIRECTOR REGIONAL	FECHA: 6 de Octubre 2013 INSP. FISCAL DISEÑO Argto. Guillermo Venegas
ESCALA 1:200	FORMATO A 1	Argto. José Manuel Palacios P.	LÁMINA: ES Pu 01