
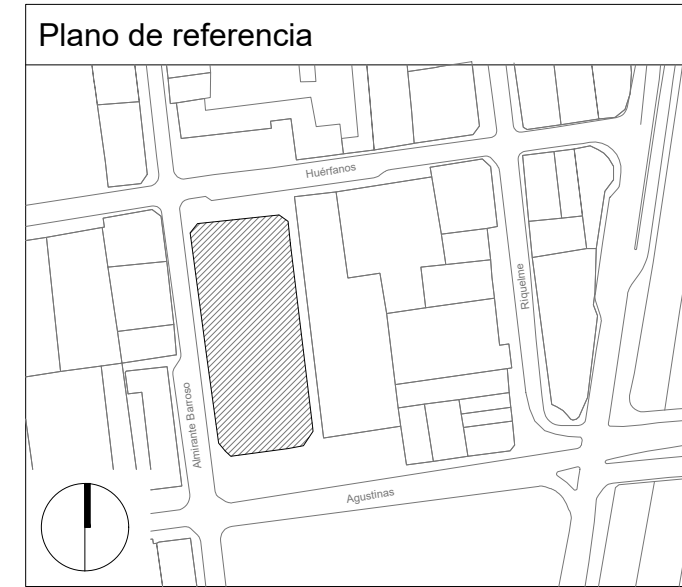


 

Modificaciones		
Índice	Fecha	Cambios
A	03/09/20	Primera emisión
B	14/09/20	Segunda emisión
C	06/10/20	Tercera emisión

Propietario	
Arzobispado de Santiago 81.795.100-7 Plaza de Armas 444, Santiago	
Representantes Legales	
Sebastián Ríos Rivas 9.668.551-0	
Bernadita Soto Velasco 11.853.234-6	
El Bosque Sur 130, Piso 15, Providencia	
Entidad Colaboradora del Proyecto de Restauración	
Fundación Basilica del Salvador 65.148.980-6	

TÁNDEM limitada	
Santiago - Chile +562 2866 66 10 contacto@tandemlimitada.cl	
Profesionales responsables	
Dino Bozzi F. Arquitecto	
Francisco Prado G. Constructor Civil	
RESTAURACIÓN Y HABILITACIÓN	
BASÍLICA DEL SALVADOR Huérfanos 1798 - Santiago Región Metropolitana	
PROYECTO PLANTA SUBTERRÁNEO	
TO	10
1838	PL
Emisor	Proyecto
1838	PL
Emisor	Proyecto

SIMBOLOGÍA	
ESPECIE	CANT.
JACARANDA <i>Jacaranda mimosifolia</i>	6
HELECHO VALDIVIANO <i>Logophora quadrifida</i>	18
HELECHO COSTILLA DE VACA <i>Beckhamia chilense</i>	53
HEDERA <i>Hedera helix</i>	17 m²
RHUS <i>Rhus copallina</i>	25
VINCA <i>Vinca minor</i>	30 m²

PAI	02
1/100	Oct. 20
Fecha	
Escala	
C	
Indice	