



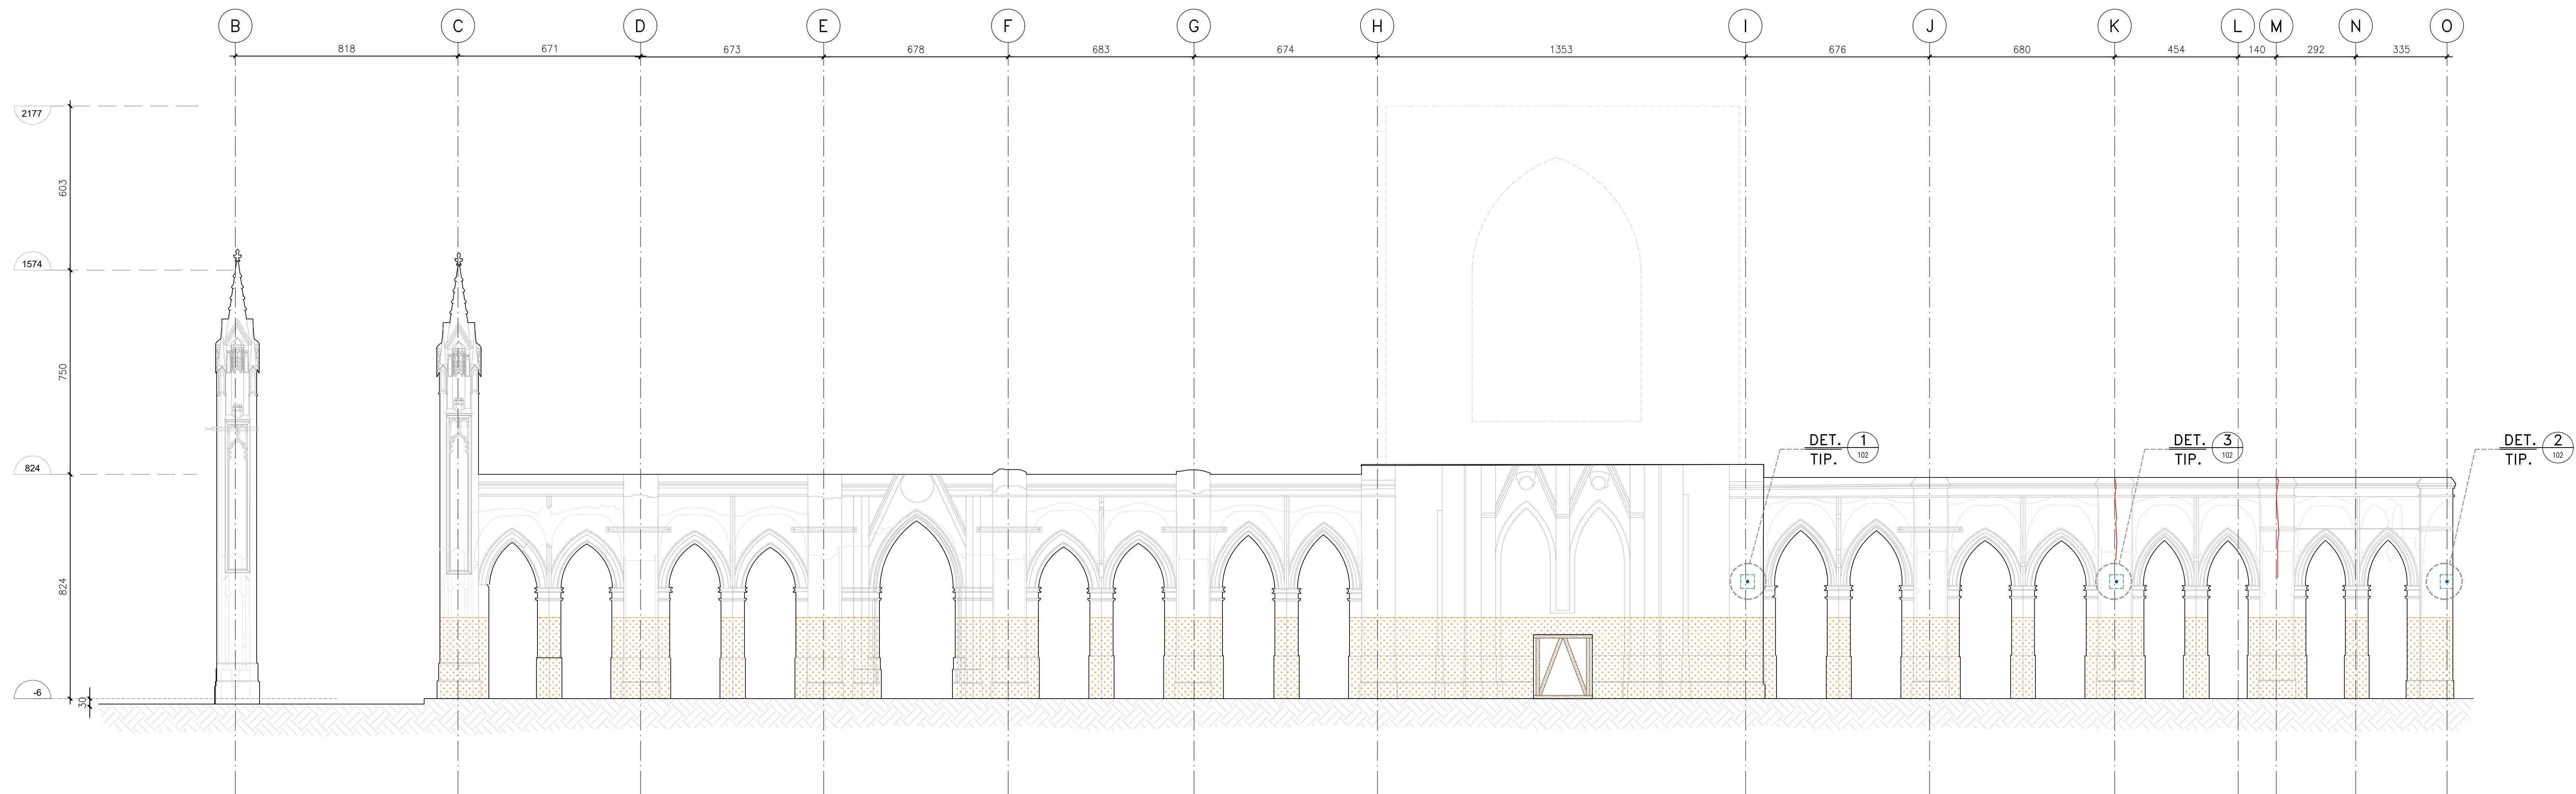

ELEVACION EJE 1
ESCALA 1:100

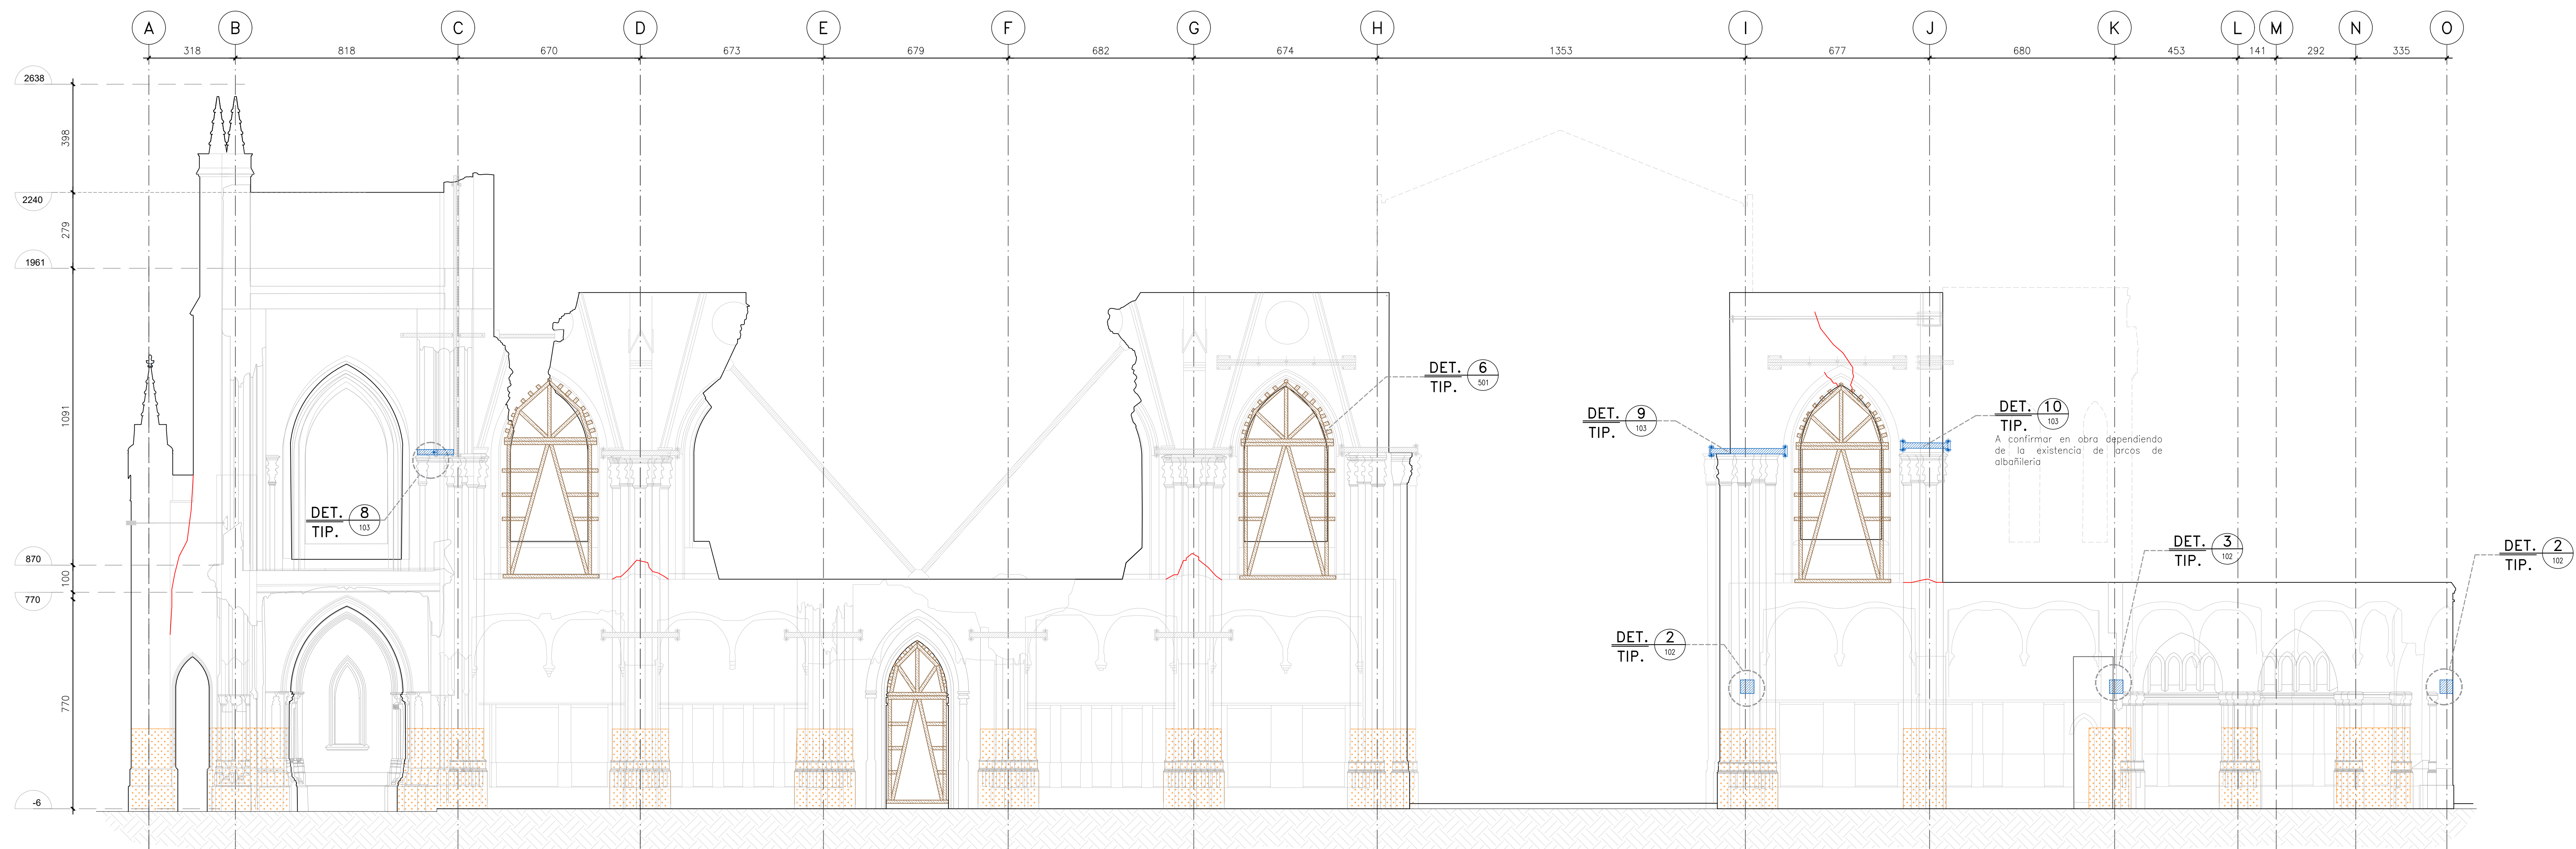

ELEVACION EJE 2
ESCALA 1:100

Nomenclatura y simbología REFUERZOS PREVIOS		
ID (Tip Material)	Intervención	Simbología
AC Ma	Alzados y cimbras de arcos y bóvedas	
IN Le	Inyecciones y consolidación	
ES Ac	Estructuras y tirantes de acero	
EE Ac	Estructura de emergencia existente de acero	
CE Fr	Confinamiento de columna existente con FRP	
De	Demolición de elementos existentes	

NOTAS:	
1.	LAS INDICACIONES DE ESTE PLANO SE DEBEN COMPLEMENTAR CON LAS ESPECIFICACIONES TÉCNICAS DEL PROYECTO, Y CON LOS PROCEDIMIENTOS INDICADOS EN LAS FICHAS DE INTERVENCIÓN (Anexo A del documento 18088-02-IF-01).
2.	LAS INDICACIONES DE ESTE PLANO SE REALIZARÁN PREVIO A LA EJECUCIÓN DE LAS OBRAS DE NUEVOS SUBTERRÁNEOS, PLANOS 18088-01-PL-EST-0111 A 1201.

D	23.02.2021	G. PERALTA M. RENDEL	CARL LUDERS	ENTREGA ETAPA DE DISEÑO
C	18.12.2020	S. SAIZ M. RENDEL	CARL LUDERS	SE MODIFICA LO INDICADO
B	04.06.2020	S. SAIZ M. RENDEL	CARL LUDERS	EMITIDO PARA REVISIÓN DEL CLIENTE
A	19.12.2019	S. SAIZ M. RENDEL	CARL LUDERS	EMITIDO PARA REVISIÓN DEL CLIENTE
Nº	FECHA	DIBUJO/REVISO	APROBÓ	DETALLE
PROYECTO DE CÁLCULO ESTRUCTURAL				
 SEISMIC PROTECTION TECHNOLOGIES Estrada 1010, Las Condes, Santiago, Chile TELÉFONO: +56 2 2607 7000 CONTACTO: info@sirve.cl WEB: www.sirve.cl  CARL LUDERS SCHWABENBERG Ingeniero CIVIL Dipl. Ing. Técnico Instituto de Construcción 3.679.1723				
PROYECTO RECUPERACIÓN BASÍLICA DEL SALVADOR				
UBICACIÓN CALLE HUERFANOS 1796 - SANTIAGO				
CLIENTE FUNDACIÓN BASÍLICA DEL SALVADOR				
CONTENIDO REFUERZOS PREVIOS - ELEVACIÓN EJES 1 Y 2				
CORRO DEL DOCUMENTO 18088-02-PL-EST-0203				REVISIÓN D
FORMATO A3		ESCALA 1 : 100	FECHA 23.02.2021	