

MONICA PEREZ & ASOCIADOS
a r q u i t e c t u r a d e l u z ®

Consultoría y Desarrollo de Proyectos de iluminación

Málaga 115 OF. 813 Las Condes, Santiago

Telefonos: 263 13 12, 228 23 38

e-mail: monica7@arquiluz.cl

PROYECTO DE ILUMINACION: 4611

RESTAURACIÓN BASÍLICA DEL SALVADOR

Edición "E"

14 de Agosto de 2020

PROYECTO

ESPECIFICACIONES TECNICAS DE ILUMINACION

PROYECTO 4611
RESTAURACION BASILICA DEL SALVADOR.

Fecha 14/08/2020
Estado **PROYECTO.** Edición **E**

INDICE.

SECCION	REFERENCIA	ESTADO
I.-	HISTORIAL.	APLICA
II.-	NOTAS IMPORTANTES.	APLICA
III.-	LUMINARIAS TECNICAS.	APLICA
IV.-	LUMINARIAS DECORATIVAS Y ESPECIALES.	APLICA
IV.- (B).	COMPLEMENTOS DE LUMINARIAS.	NO APLICA
V.-	SISTEMAS DE CONTROL Y REGULACION.	NO APLICA
VI.-	ACCESORIOS Y SISTEMAS DE MONTAJE.	NO APLICA
VII.-	DETALLES Y ESQUEMAS DE REFERENCIA.	APLICA

CONTROL DE CAMBIOS.

Nº	DESCRIPCION	FECHA
01		
02		
03		
04		
05		
06		
07		
08		
09		
10		
11		
12		
13		
14		
15		
16		
17		
18		
19		
20		

NOTA IMPORTANTE.

La información contenida en este documento es propiedad intelectual de Mónica Pérez & Asociados Ltda. De uso exclusivo de nuestro personal interno y de las personas debidamente involucradas en el desarrollo de este proyecto.
Se prohíbe la reproducción total o parcial sin autorización del contenido escrito, gráfico y de los formatos.

PROYECTO 4611

Fecha 14/08/2020

RESTAURACION BASILICA DEL SALVADOR.

Estado **PROYECTO.**

Edición E

CORRELATIVO DE PLANOS Y ESPECIFICACIONES TECNICAS DE ILUMINACION.

La edición **"E"**, de las especificaciones técnicas de iluminación, corresponde a las siguientes ediciones de los planos de iluminación.

[illegible]

E	14/08/2020	PROYECTO.	MODIFICACIONES SEGÚN COORDINACION DEL PROYECTO.
D	11/08/2020	PROYECTO.	MODIFICACIONES SEGÚN COORDINACION DEL PROYECTO.
C	13/12/2019	PROYECTO.	MODIFICACIONES SEGÚN COORDINACION DEL PROYECTO.
B	30/07/2019	COORDINACION.	MODIFICACIONES SEGÚN COORDINACION DEL PROYECTO.
A	02/07/2019	ANTEPROYECTO.	ENTREGA PROYECTO DE ILUMINACION.
EDICION	FECHA	ESTADO	OBSERVACIONES

PROYECTO 4611
RESTAURACION BASILICA DEL SALVADOR.

Fecha 14/08/2020
Estado **PROYECTO.**
Edición **E**

NOTAS IMPORTANTES DEL PROYECTO.

T01	GENERALES:
a)	Todas las cantidades indicadas en planos y/o especificaciones técnicas son de carácter informativo, siendo responsabilidad del proponente su verificación.
b)	Punto de luz: indica circuito independiente para iluminación posterior (no es una luminaria).
c)	En cada espacio todas las lámparas que requieren recambio (Led Retrofit y/o fluorescente T5) deben ser de la misma marca para que no se produzcan diferencias de temperatura (°K) y apariencia de color.
d)	En cada ítem se indican las notas relacionadas con el montaje de las luminarias.
e)	Los sistemas de regulación y de montaje, se indican en la sección "V" y "VI" de las especificaciones técnicas.
f)	La ubicación, distribución y cantidad de centros de luz indicados en el proyecto de iluminación prevalecen sobre el proyecto eléctrico.
T02	PROVEEDORES:
a)	Se debe entregar una carta de garantía por los productos suministrados, indicando de manera explícita las condiciones que aplican para su cumplimiento. También deben incluir los documentos técnicos que respalden la calidad de las luminarias, tales como certificados, ensayos nacionales y/o extranjeros y los correspondientes requeridos por la S.E.C. si existen conforme a la incorporación de nuevas tecnologías de iluminación.
b)	Todas las luminarias deben ser suministradas con las indicaciones de montaje y almacenamiento.
c)	Todos los equipos eléctricos (Fuentes de poder) deben ser entregados por el proveedor, para garantizar la compatibilidad del sistema en cada luminaria.
d)	La garantía de las luminarias no puede ser inferior a lo requerido para cada ítem.
e)	Para las luminarias con lámparas fluorescente T5, el proveedor debe entregar los todos los tubos de la misma marca, para garantizar la uniformidad en la temperatura de color de la luz. (Cuando aplique).
T03	PROPONENTE (CONTRATISTA):
a)	Las luminarias deben corresponder a las especificadas, sin variaciones en los requerimientos.
b)	No se aceptan luminarias alternativas si no es requerido por el mandante.
c)	Si es requerido el cambio de las luminarias especificadas, es responsabilidad del I.T.O. y el proyectista de iluminación la evaluación de alternativas que cumplan con los estándares de calidad requeridos para el proyecto.
d)	Las luminarias deben ser compradas con la debida anticipación para evitar problemas de suministro que alteren los plazos de la obra.
e)	Se debe solicitar muestras físicas de las luminarias, para: - Coordinación en obra de los detalles de montaje. - Revisión por parte del Mandante, Arquitectura y/o I.T.O. antes de la instalación. - Aprobación por parte del mandante arquitectura y/o proyectista.
f)	La constructora debe emitir planos y EE.TT. as Built.

PROYECTO 4611
RESTAURACION BASILICA DEL SALVADOR.

Fecha 14/08/2020

Estado **PROYECTO.**

Edición **E**

T04	INSTALADOR:
a)	Se debe respetar la ubicación y distribución de los centros de luz indicados en los planos de iluminación. La que prevalece sobre el proyecto eléctrico.
b)	En las luminarias lineales se debe considerar una caja de derivación indicada en el plano con el icono "C.E." en el término de cada cinta. Las otras luminarias cuentan con sistema de interconexión incluido.
c)	En las luminarias lineales industriales se indica el extremo de conexión, marcado con el icono "C.E.", considerando un distanciamiento que permita el radio de curvatura normativo para el cable con cubierta E.V.A.
d)	Las luminarias lineales embutidas consideran dos cables de suspensión, para anclarlas a la losa o estructura soportante.
e)	Las luminarias de sección circular consideran cables de suspensión independientes (uno para la carcasa uno para la fuente de poder y uno para el kit de emergencia (cuando aplique)).
f)	La orientación de las luminarias exteriores debe corresponder a la indicada en los esquemas de referencia.
g)	Los cables de alimentación con cubierta E.V.A deben ser de un solo color para todo el proyecto, considerando blanco o negro.
h)	Los cables de alimentación para circuito normal (Fase/Neutro/Tierra) deben ser conductores de tres cables y los que consideran circuito de emergencia (Fase/Neutro/Tierra + Fase para kit auto-energizado) deben ser de cuatro cables en el mismo conductor.
i)	Los cables de suspensión de las luminarias deben ser multi-filares y corresponder a los indicados en las especificaciones técnicas (sección "VI") y contar con las certificaciones y ensayos correspondientes.
j)	Las luminarias deben ser instaladas con la fuente de poder entregada por el proveedor para cada ítems según corresponda, para asegurar la compatibilidad del sistema.
k)	Las luminarias no deben ser conectadas directo a 220V sin fuente de poder.
l)	Se deben respetar las notas de montaje indicadas para cada ítem.
m)	Se deben utilizar todos los accesorios de montaje entregados por el proveedor, para asegurar el funcionamiento de las luminarias
n)	Para la instalación de las luminarias se deben retirar todos los elementos de embalaje que puedan estar incluidos, en especial los plásticos que cubren los difusores y fuentes de poder.
o)	Cualquier accesorio de montaje extraviado en obra debe ser sustituido por uno igual al original, en cuanto a materialidad y estética.

PROYECTO 4611
RESTAURACION BASILICA DEL SALVADOR.

Fecha 14/08/2020
Estado PROYECTO. Edición E

ITEM
O.5.1.-

9



Descripción:

Luminaria tipo spot, fija, sobrepuesta.
Cuerpo de aluminio inyectado, Difusor retraído de PMMA polimetil metacrilato transparente. Reflector de alta eficiencia con trama faceta y óptica de apertura de 60°. Tornillería de acero inoxidable. Estribo de anclaje de acero inoxidable. Sección inferior removible para instalación y registro de los componentes.
Equipo fabricado conforme a las directivas "CE" de la Unión Europea y normas americanas.
Grado de Protección IP: 54. / **Clase:** I.
Color de equipo: Blanco mate.
- Altura: 110 mm.
- Diámetro: 120 mm.

Lámpara:

Tipo: Led COB, 25W. **Temp. Color:** 3000°K. **Apertura:** 60°. **Vida útil:** 50.000 hrs.
F. luminoso: 2500 Lm. **Eficiencia:** 50 Lm/W. **I.R.C.:** > 85. **Garantía:** 5 años.

Equipo Eléctrico: (Requisitos mínimos).

Incorporado.
Driver electrónico de voltaje constante.
Grado de protección: IP20-44.
Interfaz: on/off.
Input:
Tensión alimentación AC: 85...265V. (±10%).
Frecuencia: 50 – 60 Hz.
Output:
Tensión alimentación DC: 3V...48V. (±5%).
Corriente: 350...700mA.
Operación:
Encendido y apagado: digital.
Modo stand-by: 0.1...0.5W. (±0.1W).
Factor de potencia (λ): ≥0.95.
Distorsión armónica (THD): 10% (±5%).
Temperatura ambiente (Ta): -20...+50°C.
Temperatura carcasa (Tc): máx 75 °C.

Normativas:

Seguridad: EN 61347-1, EN 61347-2-3, EN 61347-2-13.
Radio interferencias: EN 55015.
Armónicos: EN 61000-3-2.
Emisión CEM: EN 61000-3-3.
Inmunidad CEM: EN 61547.
Compatibilidad con sistemas de emergencia: EN 61347-2-3, EN 60598-2-22.
Marcado CE: Impreso en la carcasa.

Sistema: (Equipo eléctrico + Lámpara).

Consumo: 27W aprox.
El equipo eléctrico y el Led deben ser 100% compatibles.

Sistema de emergencia:

No aplica.

Sistema de control:

No aplica.

Esquemas de Referencia:

R01.

Ubicación:

Circulaciones.

Notas de montaje:

1. Las luminarias deben quedar ancladas a la losa con el kit de instalación entregado por el proveedor.

REFERENCIA TÉCNICA: Modelo: VK-SL2834.

Marca: VKLG Ltda.

Distribuidor: VKLG Ltda.

PROYECTO 4611
RESTAURACION BASILICA DEL SALVADOR.

Estado **PROYECTO.** Fecha 14/08/2020
Edición **E**

ITEM 92
O.5.2.-



Descripción:

Luminaria tipo spot dirigible, sobrepuesto.
Cuerpo cilíndrico de aluminio extruido, rotula de giro independiente, horizontal de 0° a 355° y vertical de 0° a 100°. Difusor retraído de PMMA transparente. Reflector de aluminio facetado con óptica radial, ángulo de apertura de 10°. Base de anclaje con sistema giratorio. Louver antideslumbrante con trama hexagonal.
Equipo fabricado conforme a las directivas "CE" de la Unión Europea.

Grado de Protección IP: 44. / **Clase:** I.

Color de la luminaria: Blanco mate.

- Diámetro del cilindro: 150 mm.
- Largo: 200 mm.

Lámpara:

Tipo: Led COB, 30W. **Temp. Color:** 3000°K. **Apertura:** 10°. **Vida útil:** 50.000 hrs.

F. luminoso: 3.300 Lm. **Eficiencia:** 110 Lm/W. **I.R.C.:** > 90. **Garantía:** 5 años.

Equipo Eléctrico: (Requisitos mínimos).

Incorporado.
Driver electrónico de voltaje constante.
Grado de protección: IP20-44.
Interfaz: on/off.
Input:
Tensión alimentación AC: 85...265V. (±10%).
Frecuencia: 50 – 60 Hz.
Output:
Tensión alimentación DC: 3V...48V. (±5%).
Corriente: 350...700mA.

Operación:
Encendido y apagado: digital.
Modo stand-by: 0.1...0.5W. (±0.1W).
Factor de potencia (λ): ≥0.95.
Distorsión armónica (THD): 10% (±5%).
Temperatura ambiente (Ta): -20...+50°C.
Temperatura carcasa (Tc): máx 75 °C.

Normativas:

Seguridad: EN 61347-1, EN 61347-2-3, EN 61347-2-13.
Radio interferencias: EN 55015.
Armónicos: EN 61000-3-2.
Emisión CEM: EN 61000-3-3.
Inmunidad CEM: EN 61547.
Compatibilidad con sistemas de emergencia: EN 61347-2-3, EN 60598-2-22.
Marcado CE: Impreso en la carcasa.

Sistema: (Equipo eléctrico + Lámpara).

Consumo: 32W aprox.
El equipo eléctrico y el Led deben ser 100% compatibles.

Sistema de emergencia:

No aplica.

Sistema de control:

No aplica.

Esquemas de Referencia:

R02.

Ubicación:

Nave central (alter y coro).

Notas de montaje:

1. El instalador debe considerar el sistema anclaje según superficie y materialidad donde se instalará la luminaria.
2. La altura de montaje acotada en el plano, se indica al centro de la luminaria.

REFERENCIA TÉCNICA: Modelo: VK-SL2976-SB.

Marca: VKLG Ltda.

Distribuidor: VKLG Ltda.


PROYECTO 4611
RESTAURACION BASILICA DEL SALVADOR.

Fecha 14/08/2020

Estado **PROYECTO.**

Edición **E**

ITEM 15
O.5.3.-
O.5.3.1.-
SE

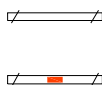

Kit emergencia:
Máx. 60W = 4.

Descripción:

Luminaria lineal, estanca, en cinta y/o individual. Colgante o sobrepuesta.
Cuerpo de policarbonato de alta resistencia, con tratamiento auto-extinguible. Difusor de policarbonato opal con 20% de transparencia. Parte superior de aluminio extruido para disipación de calor. Fuente de luz dispuesta en base de aluminio con sistema de disipador de calor. Reflector interior con Angulo de apertura de 120°. Sistema de conexión para línea continua con unión invisible. Terminales de conexión para toma de corriente e interconexión. Tornillería de acero inoxidable. Juntas de estanqueidad de silicona y prensaestopas. Clips retráctiles para fijación del sistema de montaje.

Equipo fabricado conforme a las directivas "CE" de la Unión Europea.

Grado de Protección: IP65. / **Protección eléctrica:** Clase I. / **Protección de impacto:** IK10.

Color de equipo: Estándar.

Dimensiones:

- Largo: 1200 mm. / Alto: 74 mm. / Ancho: 74 mm.

Lámpara:

Tipo: Led Linear, 40W. **Temp. color:** 3000°K. **Apertura:** 120°. **Vida útil:** 50.000 hrs.

F. luminoso: 4.400 Lm. **Eficiencia:** 110 Lm/W. **I.R.C.:** > 80. **Garantía:** 5 años.

Equipo Eléctrico: (Requisitos mínimos).

Incorporado.
Driver electrónico de voltaje constante.
Grado de protección: IP44-67.

Interfaz: on/off.

Input:

Tensión alimentación AC: 85...265V. (±10%).
Frecuencia: 50 – 60 Hz.

Output:

Tensión alimentación DC: 3V...48V. (±5%).
Corriente: 350...700mA.

Operación:

Encendido y apagado: digital.
Modo stand-by: 0.1...0.5W. (±0.1W).
Factor de potencia (λ): ≥0.95.
Distorsión armónica (THD): 10% (±5%).
Temperatura ambiente (Ta): -20...+50°C.
Temperatura carcasa (Tc): máx 75 °C.

Normativas:

Seguridad: EN 61347-1, EN 61347-2-3,
EN 61347-2-13.
Radio interferencias: EN 55015.
Armónicos: EN 61000-3-2.
Emisión CEM: EN 61000-3-3.
Inmunidad CEM: EN 61547.
Compatibilidad con sistemas de emergencia:
EN 61347-2-3, EN 60598-2-22.
Marcado CE: Impreso en la carcasa.

Sistema: (Equipo eléctrico + Lámpara).

Consumo: 42W aprox.

El equipo eléctrico, el Led y el kit de emergencia deben ser 100% compatibles.

Sistema de emergencia:

Kit de emergencia auto-energizado, incorporado de 1.5 horas de duración, con luz roja o verde para señal de carga y funcionamiento.

Sistema de control:

No aplica.

Esquemas de Referencia:
R03.

Ubicación:

Recintos técnicos.

Notas de montaje:

1. Las luminarias colgantes deben quedar anclada a la losa con el cable de suspensión regulable. Para complemento de normativa sísmica.
2. Las luminarias sobrepuestas deben mantener una separación mínima de 10mm, para permitir la circulación del aire y evitar la cristalización de componentes no metálicos.
3. El kit de emergencia debe ser suministrado por el proveedor de la luminaria para asegurar la compatibilidad y garantía del sistema.

REFERENCIA TÉCNICA: **Modelo:** VK-VXS SLIM-40.

Marca: VKLG Ltda.

Distribuidor: VKLG Ltda.

PROYECTO 4611
RESTAURACION BASILICA DEL SALVADOR.

Fecha 14/08/2020

Estado **PROYECTO.**

Edición **E**

ITEM 165
O.5.4.-
O.5.4.1.-
SE



Kit emergencia:
Máx. 60W = 30.

Descripción:

Luminaria tipo proyector de área, fija, sobrepuesta.
Cuerpo de aluminio inyectado. Disipador de calor estriado incluido en la parte posterior del cuerpo principal. Vidrio frontal templado transparente de 5mm de espesor. Tratamiento anticorrosivo para ambientes salinos. Reflector interior de alta eficiencia con óptica de apertura de 120°. Tornillería de acero inoxidable. Juntas de estanqueidad de silicona. Prensa-estopa para canalizaciones. Sistema de anclaje a muro para orientación fija en 0°.
Equipo fabricado conforme a las directivas "CE" de la Unión Europea.

Grado de Protección IP: 67. / **Grado de Protección IK:** 07. / **Clase:** I.

Color de la luminaria: Blanco mate.

Dimensiones:

- Largo: 298mm.
- Alto: 160mm.
- Ancho: 364 mm.

Lámpara:

Tipo: Led COB 47W. **Temp. Color:** 3000°K. **Apertura:** 120°. **Vida útil:** 50.000 hrs.
F. luminoso: 3.995 Lm. **Eficiencia:** 85 Lm/W. **I.R.C.:** > 80. **Garantía:** 5 años.

Equipo Eléctrico: (Requisitos mínimos).

Incorporado.
Driver electrónico de voltaje constante.
Grado de protección: IP44-67.
Interfaz: on/off.
Input:
Tensión alimentación AC: 85...265V. (±10%).
Frecuencia: 50 – 60 Hz.
Output:
Tensión alimentación DC: 3V...48V. (±5%).
Corriente: 350...700mA.
Operación:
Encendido y apagado: digital.
Modo stand-by: 0.1...0.5W. (±0.1W).
Factor de potencia (λ): ≥0.95.
Distorsión armónica (THD): 10% (±5%).
Temperatura ambiente (Ta): -20...+50°C.
Temperatura carcasa (Tc): máx 75 °C.

Normativas:

Seguridad: EN 61347-1, EN 61347-2-3, EN 61347-2-13.
Radio interferencias: EN 55015.
Armónicos: EN 61000-3-2.
Emisión CEM: EN 61000-3-3.
Inmunidad CEM: EN 61547.
Compatibilidad con sistemas de emergencia: EN 61347-2-3, EN 60598-2-22.
Marcado CE: Impreso en la carcasa.

Sistema: (Equipo eléctrico + Lámpara).

Consumo: 50W aprox.
El equipo eléctrico, el Led y el kit de emergencia deben ser 100% compatibles.

Sistema de emergencia:

Kit de emergencia auto-energizado, incorporado de 1.5 horas de duración, con luz roja o verde para señal de carga y funcionamiento.

Sistema de control:

No aplica.

Esquemas de Referencia:

R04, R05.

Ubicación:

Nave central (iluminación directa e indirecta).

Notas de montaje:

1. El instalador debe considerar el sistema anclaje según superficie y materialidad donde se instalará la luminaria.
2. La altura de montaje acotada en el plano, se indica al centro de la luminaria.

REFERENCIA TÉCNICA: Modelo: VK-GL571.

Marca: VKLG Ltda.

Distribuidor: VKLG Ltda.

PROYECTO 4611
RESTAURACION BASILICA DEL SALVADOR.

Fecha 14/08/2020

Estado **PROYECTO.**

Edición **E**

ITEM
O.5.5.-

50



Descripción:

Luminaria tipo proyector de área, dirigible, para uso exterior.
Cuerpo de aluminio inyectado. Estribo de anclaje de aluminio, con escala goniométrica para orientación en ángulo específico. Disipador de calor estriado incluido en la parte posterior del cuerpo principal. Vidrio frontal templado transparente, resistente a cambios de temperatura. Tratamiento anticorrosivo para ambientes salinos. Reflector de aluminio de alta pureza. Tornillería de acero inoxidable. Juntas de estanqueidad de silicona. Prensa-estopa para canalizaciones.

Luminaria fabricada conforme a las directivas "CE" de la Unión Europea.

Grado de Protección IP: 65 / **Grado de Protección IK:** 09. / **Clase:** I.

Color de la luminaria: Gris metalizado mate.

Dimensiones:

- Largo: 203 mm.
- Alto: 64 mm.
- Ancho: 176 mm.

Lámpara:

Tipo: Led Array, 30W. **Temp. Color:** 3000°K. **Apertura:** 120°. **Vida útil:** 50.000 hrs.

F. luminoso: 3.000 Lm. **Eficiencia:** 100 Lm/W. **I.R.C.:** > 80. **Garantía:** 5 años.

Equipo Eléctrico: (Requisitos mínimos).

Incorporado.

Driver electrónico de voltaje constante.

Grado de protección: IP44-67.

Interfaz: on/off.

Input:

Tensión alimentación AC: 85...265V. (±10%).

Frecuencia: 50 – 60 Hz.

Output:

Tensión alimentación DC: 3V...48V. (±5%).

Corriente: 350...700mA.

Operación:

Encendido y apagado: digital.

Modo stand-by: 0.1...0.5W. (±0.1W).

Factor de potencia (λ): ≥0.95.

Distorsión armónica (THD): 10% (±5%).

Temperatura ambiente (Ta): -20...+50°C.

Temperatura carcasa (Tc): máx 75 °C.

Normativas:

Seguridad: EN 61347-1, EN 61347-2-3, EN 61347-2-13.

Radio interferencias: EN 55015.

Armónicos: EN 61000-3-2.

Emisión CEM: EN 61000-3-3.

Inmunidad CEM: EN 61547.

Compatibilidad con sistemas de emergencia: EN 61347-2-3, EN 60598-2-22.

Marcado CE: Impreso en la carcasa.

Sistema: (Equipo eléctrico + Lámpara).

Consumo: 32W aprox.

El equipo eléctrico, el Led y el kit de emergencia deben ser 100% compatibles.

Sistema de emergencia:

No aplica.

Sistema de control:

No aplica.

Esquemas de Referencia:

R06, M03.

Ubicación:

Circulación perimetral exterior.

Notas de montaje:

1. El instalador debe considerar el sistema anclaje según superficie y materialidad donde se instalará la luminaria.
2. La altura de montaje acotada en el plano, se indica al centro de la luminaria.
3. Para instalación en talud patio exterior. Ver fichas H03 (Sección VII). Donde se indican los esquemas de referencia y detalles de montaje.

REFERENCIA TÉCNICA: Modelo: VK-FL7030.

Marca: VKLG Ltda.

Distribuidor: VKLG Ltda.

PROYECTO 4611
RESTAURACION BASILICA DEL SALVADOR.

Fecha 14/08/2020

Estado **PROYECTO.**

Edición **E**

ITEM
O.5.6.-

53



Descripción:

Luminaria tipo proyector spot, sobrepuesta dirigible, para uso exterior.
Cuerpo de aluminio inyectado. Estribo de anclaje de aluminio, con escala goniométrica para orientación en ángulo específico. Disipador de calor estriado incluido en la parte posterior del cuerpo principal. Vidrio frontal templado transparente, resistente a cambios de temperatura. Tratamiento anticorrosivo para ambientes salinos. Visera corta-flujo. Tornillería de acero inoxidable. Juntas de estanqueidad de silicona. Prensa-estopa para canalizaciones.
Luminaria fabricada conforme a las directivas "CE" de la Unión Europea.

Grado de Protección IP: 66. / **Grado de Protección IK:** 06. / **Clase:** I.

Color de la luminaria: Gris metalizado mate.

Dimensiones:

- Largo: 146mm.
- Ancho: 127 mm.
- Alto: 362

Lámpara:

Tipo: Led Array, 28W. **Temp. Color:** 3000°K. **Apertura:** 12°. **Vida útil:** 50.000 hrs.

F. luminoso: 2.324 Lm. **Eficiencia:** 83 Lm/W. **I.R.C.:** > 80. **Garantía:** 5 años.

Equipo Eléctrico: (Requisitos mínimos).

Incorporado.
Driver electrónico de voltaje constante.
Grado de protección: IP44-67.
Interfaz: on/off.
Input:
Tensión alimentación AC: 85...265V. (±10%).
Frecuencia: 50 – 60 Hz.
Output:
Tensión alimentación DC: 3V...48V. (±5%).
Corriente: 350...700mA.
Operación:
Encendido y apagado: digital.
Modo stand-by: 0.1...0.5W. (±0.1W).
Factor de potencia (λ): ≥0.95.
Distorsión armónica (THD): 10% (±5%).
Temperatura ambiente (Ta): -20...+50°C.
Temperatura carcasa (Tc): máx 75 °C.

Normativas:

Seguridad: EN 61347-1, EN 61347-2-3,
EN 61347-2-13.
Radio interferencias: EN 55015.
Armónicos: EN 61000-3-2.
Emisión CEM: EN 61000-3-3.
Inmunidad CEM: EN 61547.
Compatibilidad con sistemas de emergencia:
EN 61347-2-3, EN 60598-2-22.
Marcado CE: Impreso en la carcasa.

Sistema: (Equipo eléctrico + Lámpara).

Consumo: 30W aprox.
El equipo eléctrico, el Led y el kit de emergencia deben ser 100% compatibles.

Sistema de emergencia:

No aplica.

Sistema de control:

No aplica.

Esquemas de Referencia:

R07, R15.

Ubicación:

Fachadas.

Notas de montaje:

1. El instalador debe considerar el sistema anclaje según superficie y materialidad donde se instalará la luminaria.
2. La altura de montaje acotada en el plano, se indica al centro de la luminaria.

REFERENCIA TÉCNICA: Modelo: VK-SQR500.

Marca: VKLG Ltda.

Distribuidor: VKLG Ltda.

PROYECTO 4611
RESTAURACION BASILICA DEL SALVADOR.

Estado **PROYECTO.** Fecha 14/08/2020
Edición **E**

ITEM
O.5.7.-

63

Descripción:

Luminaria lineal tipo proyector, sobrepuesta dirigible. Para uso exterior. Cuerpo de aluminio extruido, tapas finales de aluminio inyectado. Tratamiento anticorrosivo para ambientes salinos. Vidrio frontal templado de 5.5mm de espesor con borde esmerilado, resistente a cambios bruscos de temperatura. Lentes de policarbonato transparente con óptica parabólica de 60° de apertura. Tornillería de acero inoxidable. Visera lineal Visera corta-flujo. Juntas de estanqueidad de silicona y prensaestopas. Pedestales con escala goniométrica orientable para anclaje a muro o piso. Equipo fabricado conforme a las directivas "CE" de la Unión Europea.

Grado de Protección IP: 65. / **Grado de Protección IK:** 09. / **Clase:** I.

Color de la luminaria: Gris metalizado mate.

Dimensiones:

- Largo: 1100mm.
- Ancho: 52 mm.
- Profundidad: 52 mm.
- Alto conjunto: 125 mm. (aprox).



Lámpara:

Tipo: Led COB, 45W. **Temp. color:** 3000°K. **Apertura:** 15x60°. **Vida útil:** 50.000 hrs.

F. luminoso: 3.825 Lm. **Eficiencia:** 85 Lm/W. **I.R.C.:** > 85. **Garantía:** 5 años.

Equipo Eléctrico: (Requisitos mínimos).

Incorporado.
Driver electrónico de voltaje constante.
Grado de protección: IP44-67.
Interfaz: on/off.
Input:
Tensión alimentación AC: 85...265V. (±10%).
Frecuencia: 50 – 60 Hz.
Output:
Tensión alimentación DC: 3V...48V. (±5%).
Corriente: 350...700mA.
Operación:
Encendido y apagado: digital.
Modo stand-by: 0.1...0.5W. (±0.1W).
Factor de potencia (λ): ≥0.95.
Distorsión armónica (THD): 10% (±5%).
Temperatura ambiente (Ta): -20...+50°C.
Temperatura carcasa (Tc): máx 75 °C.

Normativas:

Seguridad: EN 61347-1, EN 61347-2-3, EN 61347-2-13.
Radio interferencias: EN 55015.
Armónicos: EN 61000-3-2.
Emisión CEM: EN 61000-3-3.
Inmunidad CEM: EN 61547.
Compatibilidad con sistemas de emergencia: EN 61347-2-3, EN 60598-2-22.
Marcado CE: Impreso en la carcasa.

Sistema: (Equipo eléctrico + Lámpara).

Consumo: 48W aprox.
El equipo eléctrico, el Led y el kit de emergencia deben ser 100% compatibles.

Sistema de emergencia:

No aplica.

Sistema de control:

No aplica.

Esquemas de Referencia:

R08, R09.

Ubicación:

Fachadas.

Notas de montaje:

1. El instalador debe considerar el sistema anclaje según superficie y materialidad donde se instalará la luminaria.
2. La luminaria debe ser fijada el piso con pernos de anclaje según las indicaciones del proveedor.

REFERENCIA TÉCNICA: Modelo: VK-SL9200.

Marca: VKLG Ltda.

Distribuidor: VKLG Ltda.

PROYECTO 4611
RESTAURACION BASILICA DEL SALVADOR.

Fecha 14/08/2020
Estado PROYECTO. Edición E

ITEM
O.5.8.-

9



Descripción:

Luminaria, tipo pagoda, en poste metálico.
Cuerpo cilíndrico de aluminio extruido. Cabezal superior de aluminio fundido a alta presión, unida al mástil principal con un soporte vertical de aluminio. Fuente de luz con emisión de luz directa, difusor de vidrio transparente con tratamiento térmico. Terminación en polvo epoxi-termofijada con tratamiento anticorrosivo para ambientes salinos y protección UV. Tornillería de acero inoxidable, prensa-estopa y juntas de estanqueidad de silicona.
Equipo fabricado conforme a las directivas "CE" de la Unión Europea y normas americanas.

Grado de Protección IP: 66. / **Grado de Protección IK:** 09. / **Clase:** I.

Color de equipo: Gris mate o negro mate.

Dimensiones del cabezal:

- Ancho: 490 mm.
- Largo: 490 mm.
- Alto: 570 mm. (aprox).

Lámpara:

Tipo: Led COB 50W. **Temp. Color:** 3000°K. **Apertura:** 90° vertical. **Vida útil:** 100.000 hrs.
360° Horizontal.

F. luminoso: 7.500 Lm. **Eficiencia:** 150 Lm/W. **I.R.C.:** > 80. **Garantía:** 5 años.

Equipo Eléctrico: (Requisitos mínimos).

Incorporado.
Driver electrónico de voltaje constante.
Grado de protección: IP44-67.

Interfaz: on/off.

Input:

Tensión alimentación AC: 85...265V. (±10%).
Frecuencia: 50 – 60 Hz.

Output:

Tensión alimentación DC: 3V...48V. (±5%).
Corriente: 350...700mA.

Operación:

Encendido y apagado: digital.
Modo stand-by: 0.1...0.5W. (±0.1W).
Factor de potencia (λ): ≥0.95.
Distorsión armónica (THD): 10% (±5%).
Temperatura ambiente (Ta): -20...+50°C.
Temperatura carcasa (Tc): máx 75 °C.

Normativas:

Seguridad: EN 61347-1, EN 61347-2-3,
EN 61347-2-13.
Radio interferencias: EN 55015.
Armónicos: EN 61000-3-2.
Emisión CEM: EN 61000-3-3.
Inmunidad CEM: EN 61547.
Compatibilidad con sistemas
de emergencia: EN 61347-2-3, EN 60598-2-22.
Marcado CE: Impreso en la carcasa.

Sistema: (Equipo eléctrico + Lámpara).

Consumo: 55W aprox.
El equipo eléctrico, el Led y el kit de emergencia deben ser 100% compatibles.

Sistema de emergencia:

No aplica.

Sistema de control:

No aplica.

Sistema de anclaje:

E400-P:

Poste metálico galvanizado en caliente, sección circular Ø76mm, esp. 4mm. 4.00mt. de altura, con canastillo de anclaje.

Esquemas de Referencia:

M01, M02.

Ubicación:

Patio exterior.

Notas de montaje:

1. Ver fichas H01 y H02 (Sección VII). Donde se indican los esquemas de referencia y detalles de montaje.

REFERENCIA TÉCNICA: Modelo: VK-ETN-50.

Marca: VKLG Ltda.

Distribuidor: VKLG Ltda.

PROYECTO 4611

Fecha 14/08/2020

RESTAURACION BASILICA DEL SALVADOR.

Estado **PROYECTO.**

Edición **E**

ITEM
O.5.9.-

40



Descripción:

Luminaria tipo cilindro, emisión de luz directa e indirecta. Para uso exterior. Cuerpo cilíndrico de aluminio extruido, bisel y caja de conexión de aluminio inyectado. Reflector interior parabólico de aluminio facetado, con óptica radial. Vidrio frontal templado transparente, resistente a cambios de temperatura. Tornillería de acero inoxidable. Estribo de anclaje de acero galvanizado ubicado en la caja de conexión. Tratamiento anticorrosivo para ambientes salinos. Bisel superior e inferior removible para registro y conexión de los componentes eléctricos. Juntas de estanqueidad de goma de alta resistencia y prensa-estopas.

Equipo fabricado conforme a las directivas "CE" de la Unión Europea.

Grado de Protección IP: 65. / **Grado de Protección IK:** 08. / **Clase:** I.

Color de la luminaria: Gris metalizado mate.

Dimensiones del cilindro:

- Alto: 350 mm.
- Diámetro: 180 mm.
- Profundidad: 250 mm. (aprox).

Lámpara:

Tipo: Led COB, 2/26W. **Temp. color:** 3000°K. **Apertura:** 24°. **Vida útil:** 50.000 hrs.

F. luminoso: 4.680 Lm. **Eficiencia:** 90 Lm/W. **I.R.C.:** > 85. **Garantía:** 5 años.

Equipo Eléctrico: (Requisitos mínimos).

Incorporado.
Driver electrónico de voltaje constante.
Grado de protección: IP44-67.
Interfaz: on/off.
Input:
Tensión alimentación AC: 85...265V. (±10%).
Frecuencia: 50 – 60 Hz.
Output:
Tensión alimentación DC: 3V...48V. (±5%).
Corriente: 350...700mA.
Operación:
Encendido y apagado: digital.
Modo stand-by: 0.1...0.5W. (±0.1W).
Factor de potencia (λ): ≥0.95.
Distorsión armónica (THD): 10% (±5%).
Temperatura ambiente (Ta): -20...+50°C.
Temperatura carcasa (Tc): máx 75 °C.

Normativas:

Seguridad: EN 61347-1, EN 61347-2-3, EN 61347-2-13.
Radio interferencias: EN 55015.
Armónicos: EN 61000-3-2.
Emisión CEM: EN 61000-3-3.
Inmunidad CEM: EN 61547.
Compatibilidad con sistemas de emergencia: EN 61347-2-3, EN 60598-2-22.
Marcado CE: Impreso en la carcasa.

Sistema: (Equipo eléctrico + Lámpara).

Consumo: 55W aprox.
El equipo eléctrico, el Led y el kit de emergencia deben ser 100% compatibles.

Sistema de emergencia:

No aplica.

Sistema de control:

No aplica.

Esquemas de Referencia:

R10.

Ubicación:

Fachadas.

Notas de montaje:

1. El instalador debe considerar el sistema anclaje según superficie y materialidad donde se instalará la luminaria.
2. La altura de montaje acotada en el plano, se indica al centro de la luminaria.

REFERENCIA TÉCNICA: Modelo: VK-WDL556-UD.

Marca: VKLG Ltda.

Distribuidor: VKLG Ltda.

PROYECTO 4611
RESTAURACION BASILICA DEL SALVADOR.

Estado **PROYECTO.** Fecha 14/08/2020
Edición **E**

ITEM 23
O.5.10.-
O.5.10.1.-
SE



Kit emergencia:
Máx. 60W = 8.

Descripción:

Luminaria tipo spot, embutida en piso.
Cuerpo de aluminio inyectado, bisel de acero inoxidable, vidrio de protección templado opal, resistente cambios de temperatura. Tratamiento anticorrosivo. Sellos herméticos de silicona. Caja de empotramiento de PVC de alta resistencia. Carga máxima de resistencia 3.000kg con velocidad máxima de desplazamiento de 25km/h. Equipo eléctrico incorporado. Equipo fabricado conforme a las directivas "CE" de la Unión Europea.

Grado de Protección IP: 67. / **Grado de Protección IK:** 09. / **Clase:** II.

Color del bisel: Metálico.

Color del equipo: Negro.

Dimensiones del equipo:

- Alto: 200 mm. / Diámetro cuerpo: 130 mm. / Diámetro bisel: 148mm.

Dimensiones de la caja de empotramiento.

- Alto: 250 mm. / Diámetro: 140 mm. (aprox).

Lámpara:

Tipo: Led COB 10W. **Temp. Color:** 3000°K. **Apertura:** 30°. **Vida útil:** 50.000 hrs.

F. luminoso: 850 Lm. **Eficiencia:** 85 Lm/W. **I.R.C.:** > 80. **Garantía:** 5 años.

Equipo Eléctrico: (Requisitos mínimos).

Incorporado.
Driver electrónico de voltaje constante.
Grado de protección: IP44-67.

Interfaz: on/off.

Input:

Tensión alimentación AC: 85...265V. (±10%).
Frecuencia: 50 – 60 Hz.

Output:

Tensión alimentación DC: 3V...48V. (±5%).
Corriente: 350...700mA.

Operación:

Encendido y apagado: digital.
Modo stand-by: 0.1...0.5W. (±0.1W).
Factor de potencia (λ): ≥0.95.
Distorsión armónica (THD): 10% (±5%).
Temperatura ambiente (Ta): -20...+50°C.
Temperatura carcasa (Tc): máx 75 °C.

Normativas:

Seguridad: EN 61347-1, EN 61347-2-3,
EN 61347-2-13.
Radio interferencias: EN 55015.
Armónicos: EN 61000-3-2.
Emisión CEM: EN 61000-3-3.
Inmunidad CEM: EN 61547.
Marcado CE: Impreso en la carcasa.

Sistema: (Equipo eléctrico + Lámpara).

Consumo: 12W aprox.
El equipo eléctrico, el Led y el kit de emergencia deben ser 100% compatibles.

Sistema de emergencia:

Kit de emergencia auto-energizado, incorporado de 1.5 horas de autonomía, con luz roja o verde para señal de carga y funcionamiento.

Sistema de control:

No aplica.

Esquemas de Referencia:
R11.

Ubicación:
Subterráneo.

Notas de montaje:

1. Confirmar altura disponible y dimensiones de empotramiento con muestra física de la luminaria.
2. Considerar impermeabilización para el vano de empotramiento.
3. Cuando aplique según el tipo de superficie, la caja de empotramiento debe quedar instalada cuando se construya la obra gruesa.
4. El proveedor debe entregar las instrucciones de montaje para la instalación de la luminaria.

REFERENCIA TÉCNICA: Modelo: VK-ALT2210T.

Marca: VKLG Ltda.

Distribuidor: VKLG Ltda.

PROYECTO 4611
RESTAURACION BASILICA DEL SALVADOR.

Estado **PROYECTO.** Fecha 14/08/2020
Edición **E**

ITEM
O.5.11.-

21



Descripción:

Luminaria de luz rasante, embutida en muro.
Cuerpo y bisel de aluminio inyectado. Ventana frontal de apertura con sistema antideslumbrante y ángulo de 44° de apertura. Emisión de luz rasante a piso. Difusor de vidrio templado con textura traslucida. Sellos herméticos de silicona. Tornillería de acero inoxidable. Caja de empotramiento de PVC.

Equipo fabricado conforme a las directivas "CE" de la Unión Europea.

Grado de Protección IP: 65. / **Grado de Protección IK:** 07. / **Clase:** I.

Color del bisel: Gris mate.

Dimensiones bisel.

Alto: 171mm. / Ancho: 105mm. / Bisel: 5mm.

Dimensiones de la caja de empotramiento.

Alto: 160mm. / Ancho: 90mm. / Profundidad: 65mm. (verificar con muestra física).

Lámpara:

Tipo: Led Multi-led, **Temp. Color:** 3000°K. **Apertura:** 44°. **Vida útil:** 50.000 hrs. 3W.

F. luminoso: 185 Lm. **Eficiencia:** 67 Lm/W. **I.R.C.:** > 80. **Garantía:** 5 años.

Equipo Eléctrico: (Requisitos mínimos).

Incorporado.
Driver electrónico de voltaje constante.
Grado de protección: IP44-67.

Interfaz: on/off.

Input:

Tensión alimentación AC: 85...265V. (±10%).
Frecuencia: 50 – 60 Hz.

Output:

Tensión alimentación DC: 3V...48V. (±5%).
Corriente: 350...700mA.

Operación:

Encendido y apagado: digital.
Modo stand-by: 0.1...0.5W. (±0.1W).
Factor de potencia (λ): ≥0.95.
Distorsión armónica (THD): 10% (±5%).
Temperatura ambiente (Ta): -20...+50°C.
Temperatura carcasa (Tc): máx 75 °C.

Normativas:

Seguridad: EN 61347-1, EN 61347-2-3,
EN 61347-2-13.

Radio interferencias: EN 55015.

Armónicos: EN 61000-3-2.

Emisión CEM: EN 61000-3-3.

Inmunidad CEM: EN 61547.

Marcado CE: Impreso en la carcasa.

Sistema: (Equipo eléctrico + Lámpara).

Consumo: 5W aprox.

El equipo eléctrico, el Led y el kit de emergencia deben ser 100% compatibles.

Sistema de emergencia:

No aplica.

Sistema de control:

No aplica.

Esquemas de Referencia:

R12.

Ubicación:

Subterráneo.

Notas de montaje:

1. Confirmar altura disponible y dimensiones de empotramiento con muestra física de la luminaria.
2. Considerar impermeabilización para el vano de empotramiento.
3. Cuando aplique según el tipo de superficie, la caja de empotramiento debe quedar instalada cuando se construya la obra gruesa.
4. El proveedor debe entregar las instrucciones de montaje para la instalación de la luminaria.

REFERENCIA TÉCNICA: Modelo: VK-SL3692.

Marca: VKLG Ltda.

Distribuidor: VKLG Ltda.

PROYECTO 4611
RESTAURACION BASILICA DEL SALVADOR.

Fecha 14/08/2020
Estado PROYECTO. Edición E

ITEM
O.5.12.-

15



Descripción:

Luminaria lineal tipo spot, dirigible, sobrepuesto.
Cuerpo de aluminio inyectado. Placa de anclaje con rotula de giro horizontal de 0° a 355°, rotula de giro vertical de -60° a 180°. Sistema antideslumbrante de policarbonato negro. Difusor de PMMA transparente retraído. Reflector múltiple facetado con óptica de 10°. Tornillería de acero inoxidable.
Equipo fabricado conforme a las directivas "CE" de la Unión Europea.
Grado de Protección: IP44. / **Protección eléctrica:** Clase I.
Color de la luminaria: Blanco mate.

Dimensiones:

- Largo: 184 mm.
- Ancho: 33 mm.
- Alto: 174mm.

Lámpara:

Tipo: Led COB, 16W. **Temp. Color:** 3000°K. **Apertura:** 40°. **Vida útil:** 50.000 hrs.

F. luminoso: 960 Lm. **Eficiencia:** 60 Lm/W. **I.R.C.:** > 85. **Garantía:** 7 años.

Equipo Eléctrico: (Requisitos mínimos).

Remoto (±50cm).
Driver electrónico de voltaje constante.
Grado de protección: IP20-44.
Interfaz: on/off.
Input:
Tensión alimentación AC: 85...265V. (±10%).
Frecuencia: 50 – 60 Hz.
Output:
Tensión alimentación DC: 3V...48V. (±5%).
Corriente: 350...700mA.
Operación:
Encendido y apagado: digital.
Modo stand-by: 0.1...0.5W. (±0.1W).
Factor de potencia (λ): ≥0.95.
Distorsión armónica (THD): 10% (±5%).
Temperatura ambiente (Ta): -20...+50°C.
Temperatura carcasa (Tc): máx 75 °C.

Normativas:

Seguridad: EN 61347-1, EN 61347-2-3, EN 61347-2-13.
Radio interferencias: EN 55015.
Armónicos: EN 61000-3-2.
Emisión CEM: EN 61000-3-3.
Inmunidad CEM: EN 61547.
Compatibilidad con sistemas de emergencia: EN 61347-2-3, EN 60598-2-22.
Marcado CE: Impreso en la carcasa.

Sistema: (Equipo eléctrico + Lámpara).

Consumo: 17W aprox.
El equipo eléctrico y el Led deben ser 100% compatibles.

Sistema de emergencia:

No aplica.

Sistema de control:

No aplica.

Esquemas de Referencia:

R13.

Ubicación:

Cripta.

Notas de montaje:

1. El instalador debe considerar el sistema anclaje según superficie y materialidad donde se instalará la luminaria.

REFERENCIA TÉCNICA: Modelo: VK-D900SHX.

Marca: VKLG Ltda.

Distribuidor: VKLG Ltda.


PROYECTO 4611
RESTAURACION BASILICA DEL SALVADOR.

Fecha 14/08/2020
Estado **PROYECTO.**
Edición **E**

ITEM Intermedio = 3.
O.5.13.-



Final = 2.

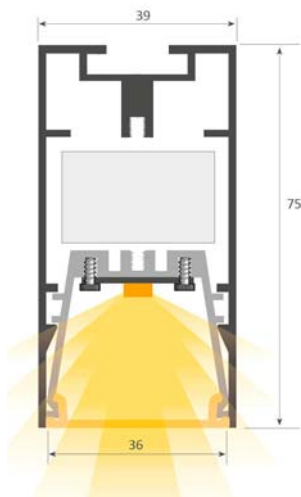

Descripción:

Luminaria lineal individual, sobrepuesta.

Cuerpo de aluminio extruido 95-98% de pureza, de 1.5 mm de espesor, tapas finales de aluminio inyectado de 2mm de espesor. Reflector de aluminio inyectado, color blanco texturado de alta reflectancia, removible para registro de componentes eléctricos y conexiones desde la parte inferior, con cable de seguridad. Partes metálicas removibles con conexión a tierra. Difusor extruido de PMMA traslucido con sistema antideslumbrante, removible. Tornillería de acero inoxidable. Baldaquín de termino.

Equipo fabricado conforme a las directivas "CE" de la Unión Europea.

Grado de Protección: IP44. / **Protección eléctrica:** Clase I.

Color de la luminaria: Gris mate.

Dimensiones:

- Luminaria individual: Largo: 1134 mm. / Alto: 75mm / Ancho: 36 mm.
- Luminaria intermedia: Largo: 1130 mm. / Alto: 75mm / Ancho: 36 mm.
- Luminaria final: Largo: 1130 mm. / Alto: 75mm / Ancho: 36 mm.

Lámpara:

Tipo: Led Linear, 17W. **Temp. Color:** 3000°K. **Apertura:** 120°. **Vida útil:** 50.000 hrs.

F. luminoso: 2.346 Lm. **Eficiencia:** 138 Lm/W. **I.R.C.:** > 80. **Garantía:** 5 años.

Equipo Eléctrico: (Requisitos mínimos).

Incorporado.

Driver electrónico de voltaje constante.

Grado de protección: IP20-44.

Interfaz: on/off.

Input:

Tensión alimentación AC: 85...265V. (±10%).

Frecuencia: 50 – 60 Hz.

Output:

Tensión alimentación DC: 3V...48V. (±5%).

Corriente: 350...700mA.

Operación:

Encendido y apagado: digital.

Modo stand-by: 0.1...0.5W. (±0.1W).

Factor de potencia (λ): ≥0.95.

Distorsión armónica (THD): 10% (±5%).

Temperatura ambiente (Ta): -20...+50°C.

Temperatura carcasa (Tc): máx 75 °C.

Normativas:

Seguridad: EN 61347-1, EN 61347-2-3,

EN 61347-2-13.

Radio interferencias: EN 55015.

Armónicos: EN 61000-3-2.

Emisión CEM: EN 61000-3-3.

Inmunidad CEM: EN 61547.

Compatibilidad con sistemas de emergencia:

EN 61347-2-3, EN 60598-2-22.

Marcado CE: Impreso en la carcasa.

Sistema: (Equipo eléctrico + lámpara).

Consumo: 18W aprox.

El equipo eléctrico, el Led y el kit de emergencia deben ser 100% compatibles.

Sistema de emergencia:

No aplica.

Sistema de control:

No aplica.

Esquemas de Referencia:

R14.

Ubicación:

Cripta.

Notas de montaje:

1. Las luminarias deben ser entregadas por el proveedor en sistemas modulares (simple, doble, triple y/o cuádruple) para optimizar el sistema de montaje y la rigidez de las cintas.
2. Las luminarias deben quedar ancladas a la estructura con la escuadra incluida en el kit de instalación.

REFERENCIA TÉCNICA: **Modelo:** VK-GL-SLIM.

Marca: VKLG Ltda.

Distribuidor: VKLG Ltda.

PROYECTO 4611

Fecha 14/08/2020

RESTAURACION BASILICA DEL SALVADOR.

Estado PROYECTO.

Edición E

ITEM
O.5.14.-

4



Descripción:

Luminaria colgante, clásica.
Cuerpo de bronce, cuentas de cristal.

Grado de Protección IP: 20. / **Clase:** I.

Color de la luminaria: Bronce.

Dimensiones aproximadas:

- Altura: 2000 mm.
- Diámetro: 1200 mm.
- Altura de colgado: 12000 mm.

Lámpara:

Tipo: Led Retrofit,
Clásica E27, X/9W.

Temp. Color:
2700...3000°K.

Apertura: 270°.
(aprox).

Vida útil: 20.000 hrs.

F. luminoso: Lm.

Eficiencia: 80 Lm/W.

I.R.C.: > 80.

Garantía: 1 año.
(Solo la carcasa).

Equipo eléctrico:

Directo a tensión de red.

Input:

Tensión de alimentación AC: 220V.

Frecuencia: 50 – 60 Hz.

Sistema: (Equipo eléctrico + lámpara).

Consumo: 200W máx.

Sistema de emergencia:

No aplica.

Sistema de control:

No aplica.

Esquemas de Referencia:

Ubicación:

Nave central.

Notas de montaje:

1. La instalación de la luminaria será de acuerdo a las indicaciones de arquitectura.

REFERENCIA TÉCNICA: Modelo: Clásica_200.

Marca: VKLG Ltda.

Distribuidor: VKLG Ltda.

PROYECTO 4611

Fecha 14/08/2020

RESTAURACION BASILICA DEL SALVADOR.

Estado PROYECTO.

Edición E

ITEM
O.5.15.-

7



Descripción:

Luminaria colgante, clásica.
Cuerpo de bronce, cuentas de cristal.

Grado de Protección IP: 20. / **Clase:** I.

Color de la luminaria: Bronce.

Dimensiones aproximadas:

- Altura: 1500 mm.
- Diámetro: 1000 mm.
- Altura de colgado: 8000 mm.

Lámpara:

Tipo: Led Retrofit,
Clásica E27, X/9W.

Temp. Color:
2700...3000°K.

Apertura: 270°.
(aprox).

Vida útil: 20.000 hrs.

F. luminoso: Lm.

Eficiencia: 80 Lm/W.

I.R.C.: > 80.

Garantía: 1 año.
(Solo la carcasa).

Equipo eléctrico:

Directo a tensión de red.

Input:

Tensión de alimentación AC: 220V.

Frecuencia: 50 – 60 Hz.

Sistema: (Equipo eléctrico + lámpara).

Consumo: 75W máx.

Sistema de emergencia:

No aplica.

Sistema de control:

No aplica.

Esquemas de Referencia:

.

Ubicación:

Acceso, capilla y sacristía.

Notas de montaje:

1. La instalación de la luminaria será de acuerdo a las indicaciones de arquitectura.

REFERENCIA TÉCNICA: Modelo: Clásica_75.

Marca: VKLG Ltda.

Distribuidor: VKLG Ltda.

PROYECTO 4611

Fecha 14/08/2020

RESTAURACION BASILICA DEL SALVADOR.

Estado PROYECTO.

Edición E

ITEM
O.5.16.-

8



Descripción:

Aplicque clásico.
Cuerpo de bronce, cuentas de cristal.

Grado de Protección IP: 20. / **Clase:** I.

Color de la luminaria: Bronce.

Dimensiones aproximadas:

- Altura: 750 mm.
- Ancho: 500 mm.
- Profundidad: 300 mm.

Lámpara:

Tipo: Led Retrofit,
Clásica E27, X/9W.

Temp. Color:
2700...3000°K.

Apertura: 270°.
(aprox).

Vida útil: 20.000 hrs.

F. luminoso: Lm.

Eficiencia: 80 Lm/W.

I.R.C.: > 80.

Garantía: 1 año.
(Solo la carcasa).

Equipo eléctrico:

Directo a tensión de red.
Input:
Tensión de alimentación AC: 220V.
Frecuencia: 50 – 60 Hz.

Sistema: (Equipo eléctrico + lámpara).
Consumo: 30W máx.

Sistema de emergencia:

No aplica.

Sistema de control:

No aplica.

Esquemas de Referencia:

.

Ubicación:

Altareos laterales.

Notas de montaje:

1. La instalación de la luminaria será de acuerdo a las indicaciones de arquitectura.

REFERENCIA TÉCNICA: Modelo: Clásico_30.

Marca: VKLG Ltda.

Distribuidor: VKLG Ltda.


PROYECTO 4611
RESTAURACION BASILICA DEL SALVADOR.

Estado **PROYECTO.**


Fecha 14/08/2020

Edición **E**


NOTA GN01: Todas las medidas de las estructuras y sistemas de anclaje indicadas en los detalles, deben ser revisadas y validadas por el especialista de cálculo del proyecto.

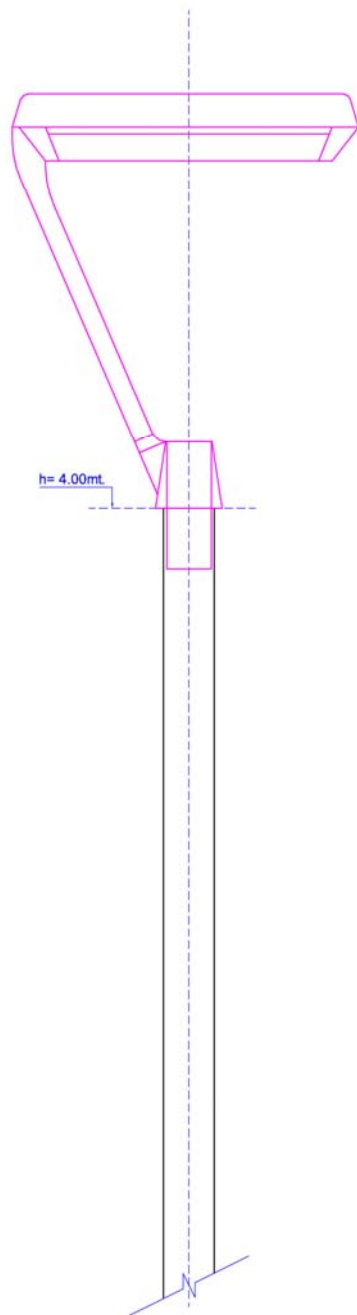


**VISTA LATERAL
CORONACION DE ANCLAJE**
esc. 1:10

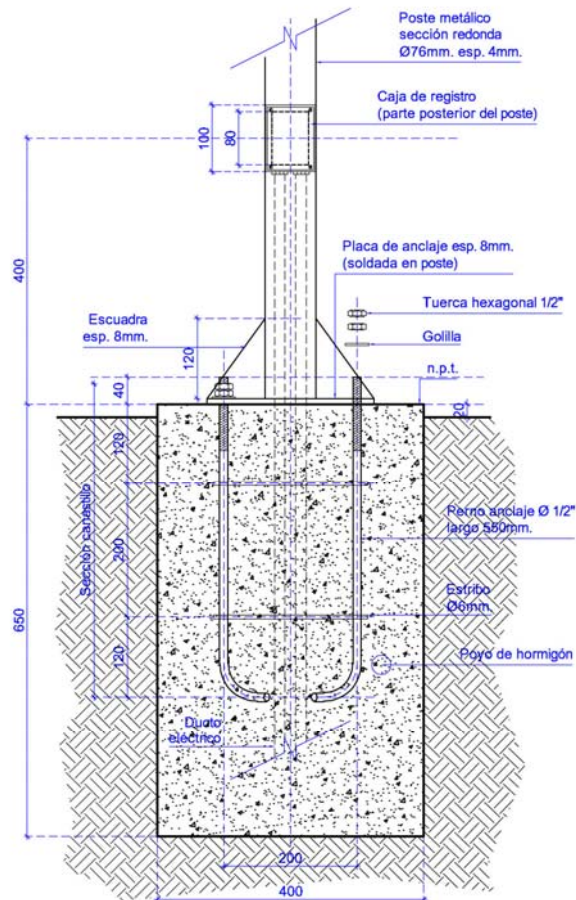


DETALLE ANCLAJE POSTE
esc. 1:10

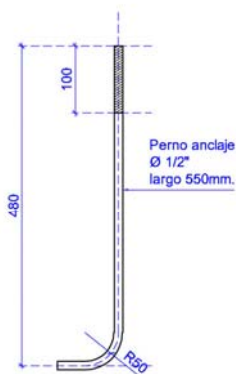

PERNO DE ANCLAJE
esc. 1:10

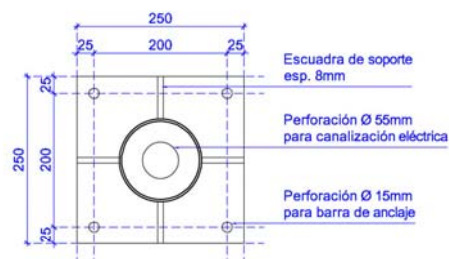

PLACA BASE DE ANCLAJE (Poste)
esc. 1:10

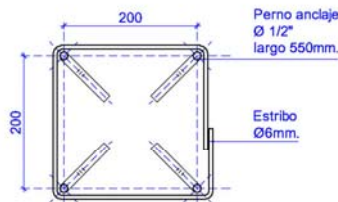

CANASTILLO DE ANCLAJE
esc. 1:10

ESQUEMA M01 / DETALLES

Poste E400-P. / Luminaria patio exterior (Anclaje para tierra).

PROYECTO
EDICIÓN F02
AGOSTO 2020

MONICA PEREZ & ASOCIADOS
arquitectura de luz ®
Consultoría y Desarrollo de Proyectos de Iluminación

Malaga 115 - OF. 813
Las Condes, Santiago
monica7@arquilluz.cl
+562 2263 1312
+562 2228 2338

PROYECTO DE ILUMINACION: 4611
RESTAURACION BASILICA DEL SALVADOR
Edición: F02 / Fecha: Agosto 2020

H01
FICHA N°

PROYECTO 4611

Fecha


14/08/2020

RESTAURACION BASILICA DEL SALVADOR.


Estado **PROYECTO.**

Edición **E**


NOTA GN01: Todas las medidas de las estructuras y sistemas de anclaje indicadas en los detalles, deben ser revisadas y validadas por el especialista de cálculo del proyecto.

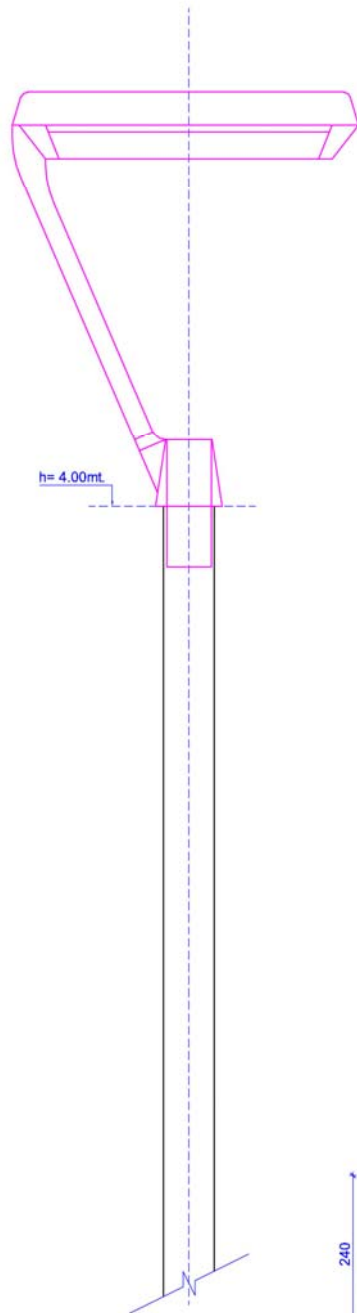


**VISTA LATERAL
CORONACION DE ANCLAJE**
esc. 1:10

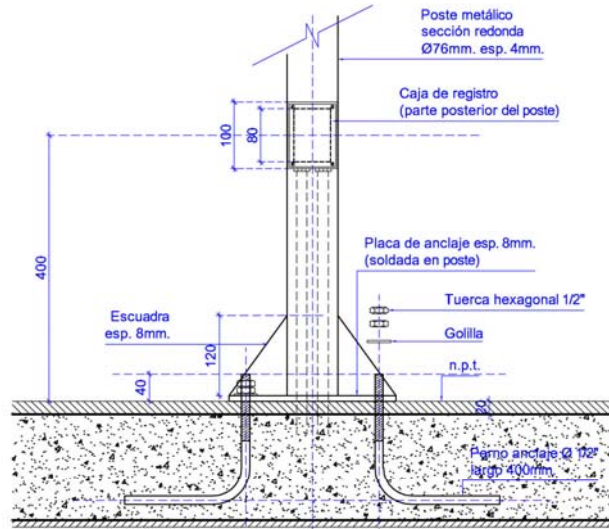


**DETALLE ANCLAJE POSTE
(EN LOSA)**
esc. 1:10

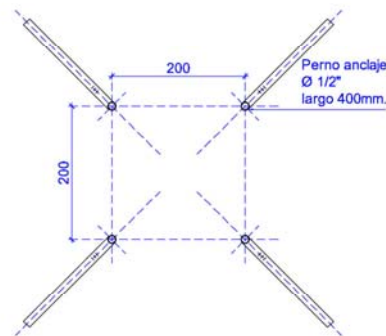

**PERNOS DE ANCLAJE POSTE
(EN LOSA)**
esc. 1:10

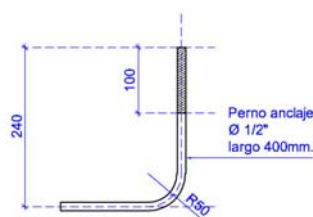

PERNO DE ANCLAJE
esc. 1:10

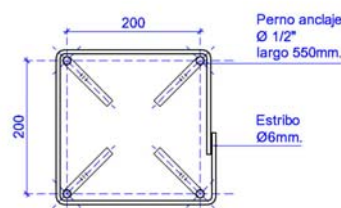

CANASTILLO DE ANCLAJE
esc. 1:10

ESQUEMA M02 / DETALLES

Poste E400-P. / Luminaria patio exterior (Anclaje para losa).

PROYECTO
EDICIÓN F02
AGOSTO / 2020

MONICA PEREZ & ASOCIADOS
arquitectura de luz ®
Consultoría y Desarrollo de Proyectos de Iluminación

Malaga 115 - OF. 813
Las Condes, Santiago
monica7@arquiliz.cl
+562 2263 1312
+562 2228 2338

PROYECTO DE ILUMINACION: 4611
RESTAURACION BASILICA DEL SALVADOR
Edición: F02 / Fecha: Agosto 2020

H02
FICHA N°


PROYECTO 4611
RESTAURACION BASILICA DEL SALVADOR.

Estado **PROYECTO.**


Fecha 14/08/2020

Edición **E**


NOTA GN01: Todas las medidas de las estructuras y sistemas de anclaje indicadas en los detalles, deben ser revisadas y validadas por el especialista de cálculo del proyecto.

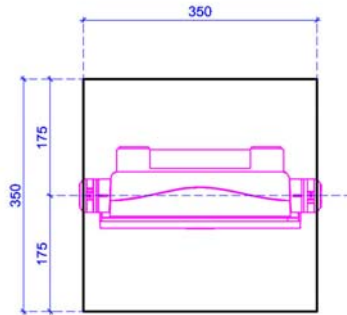

**DETALLE DE ANCLAJE
VISTA SUPERIOR**
esc. 1:10

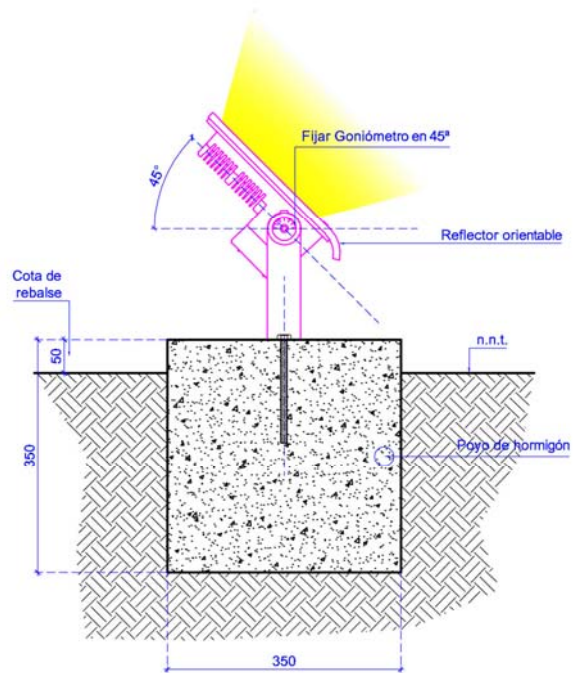

**DETALLE DE ANCLAJE
VISTA LATERAL / POSICION VALIDA**
esc. 1:10

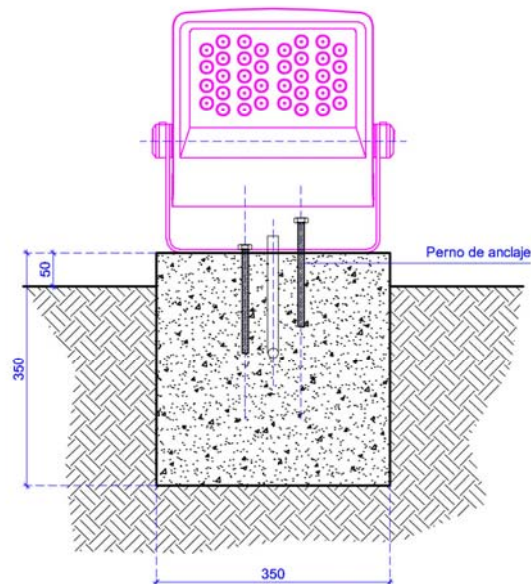

**DETALLE DE ANCLAJE
VISTA FRONTAL**
esc. 1:10

ESQUEMA M03 / DETALLES
Luminaria patio exterior "Talud" (Anclaje para tierra).

PROYECTO
EDICIÓN F02
AGOSTO / 2020

MONICA PEREZ & ASOCIADOS
arquitectura de luz ®
Consultoría y Desarrollo de Proyectos de Iluminación

Málaga 115 - OF. 813
Las Condes, Santiago
monica7@arquiliz.cl
+562 2263 1312
+562 2228 2338

PROYECTO DE ILUMINACION: 4611
RESTAURACION BASILICA DEL SALVADOR
Edición: F02 / Fecha: Agosto 2020




H03
FICHA N°

PROYECTO 4611
RESTAURACION BASILICA DEL SALVADOR.

Estado **PROYECTO.**

Fecha 14/08/2020

Edición **E**

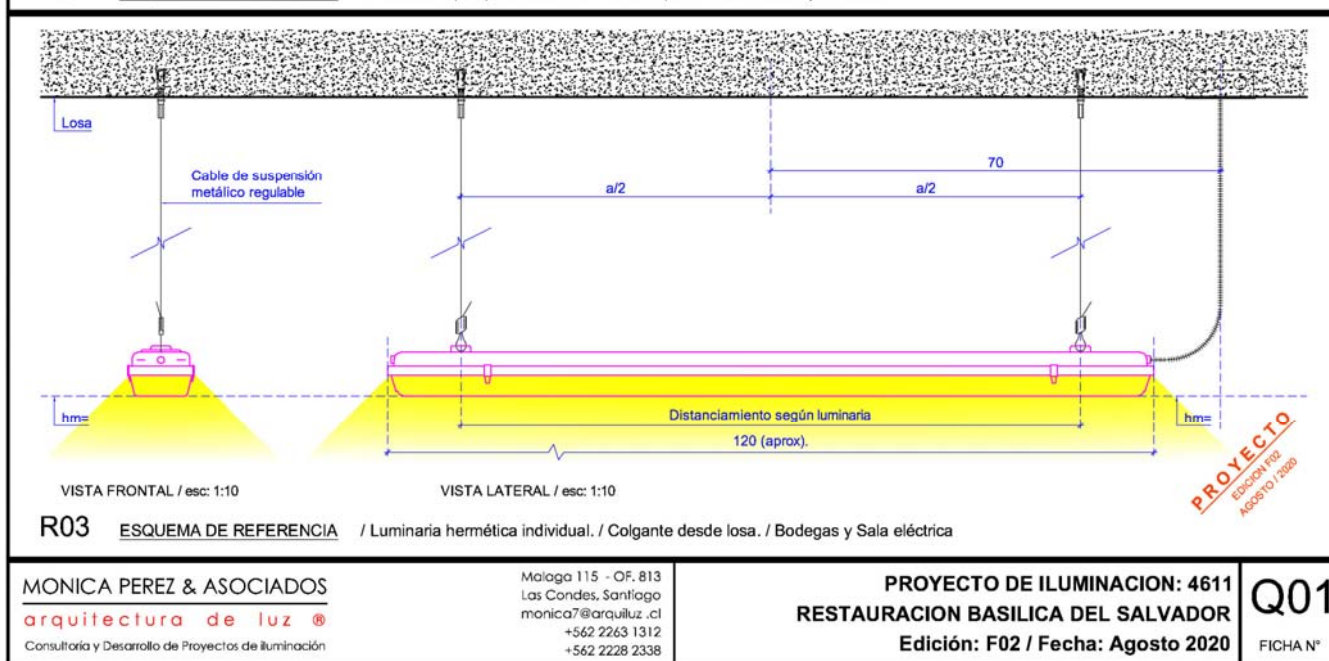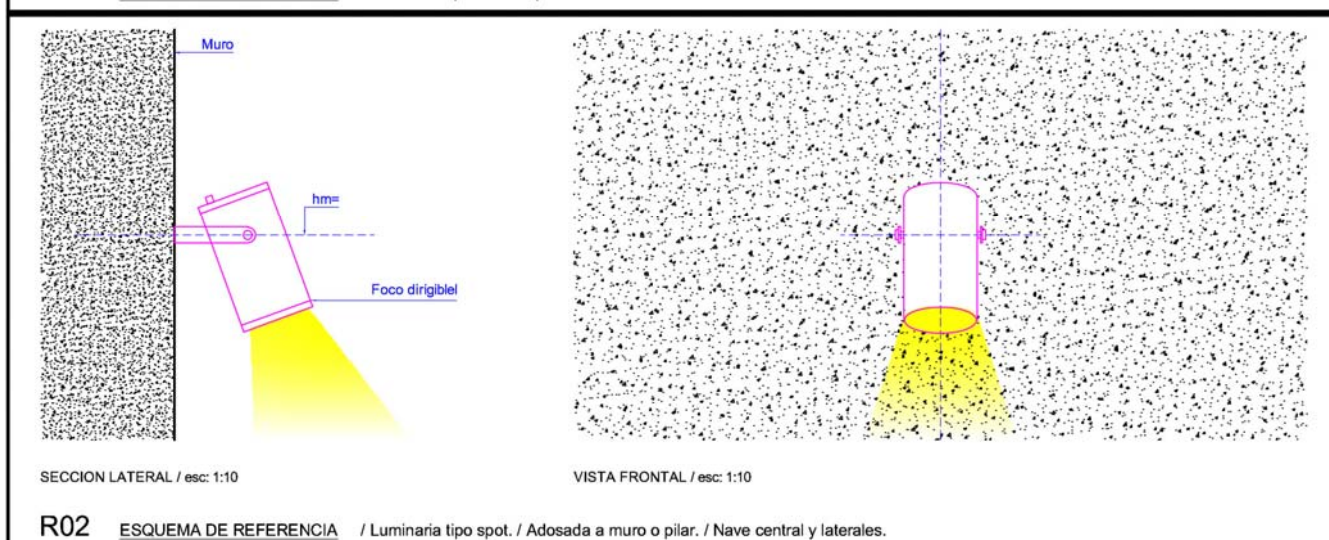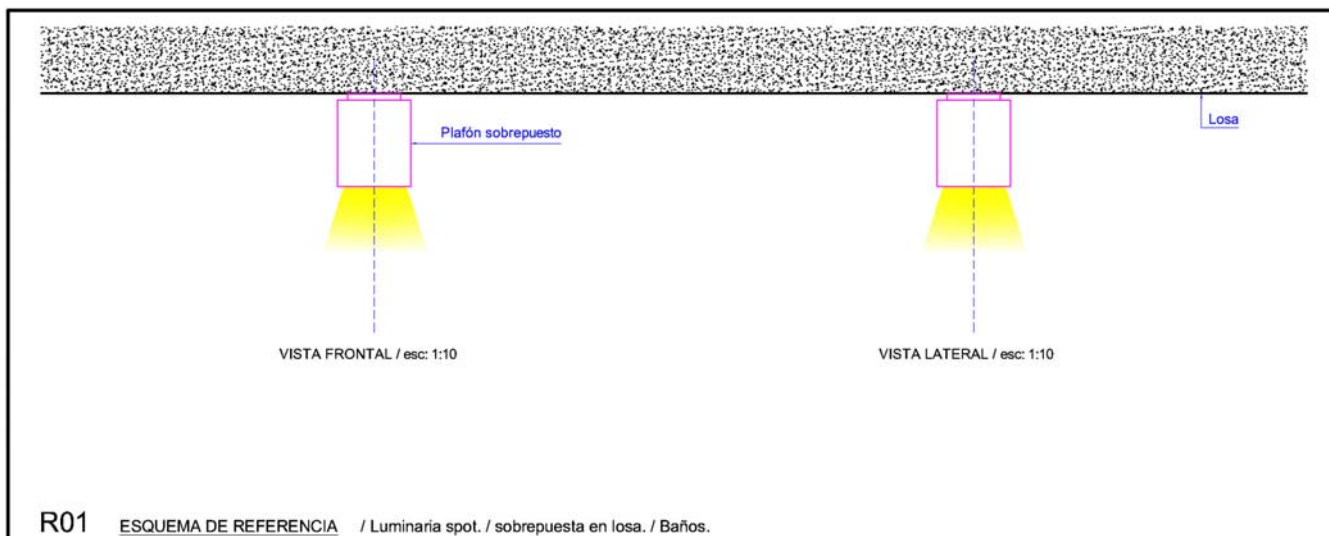


PROYECTO 4611
RESTAURACION BASILICA DEL SALVADOR.

Estado **PROYECTO.**

Fecha 14/08/2020

Edición **E**

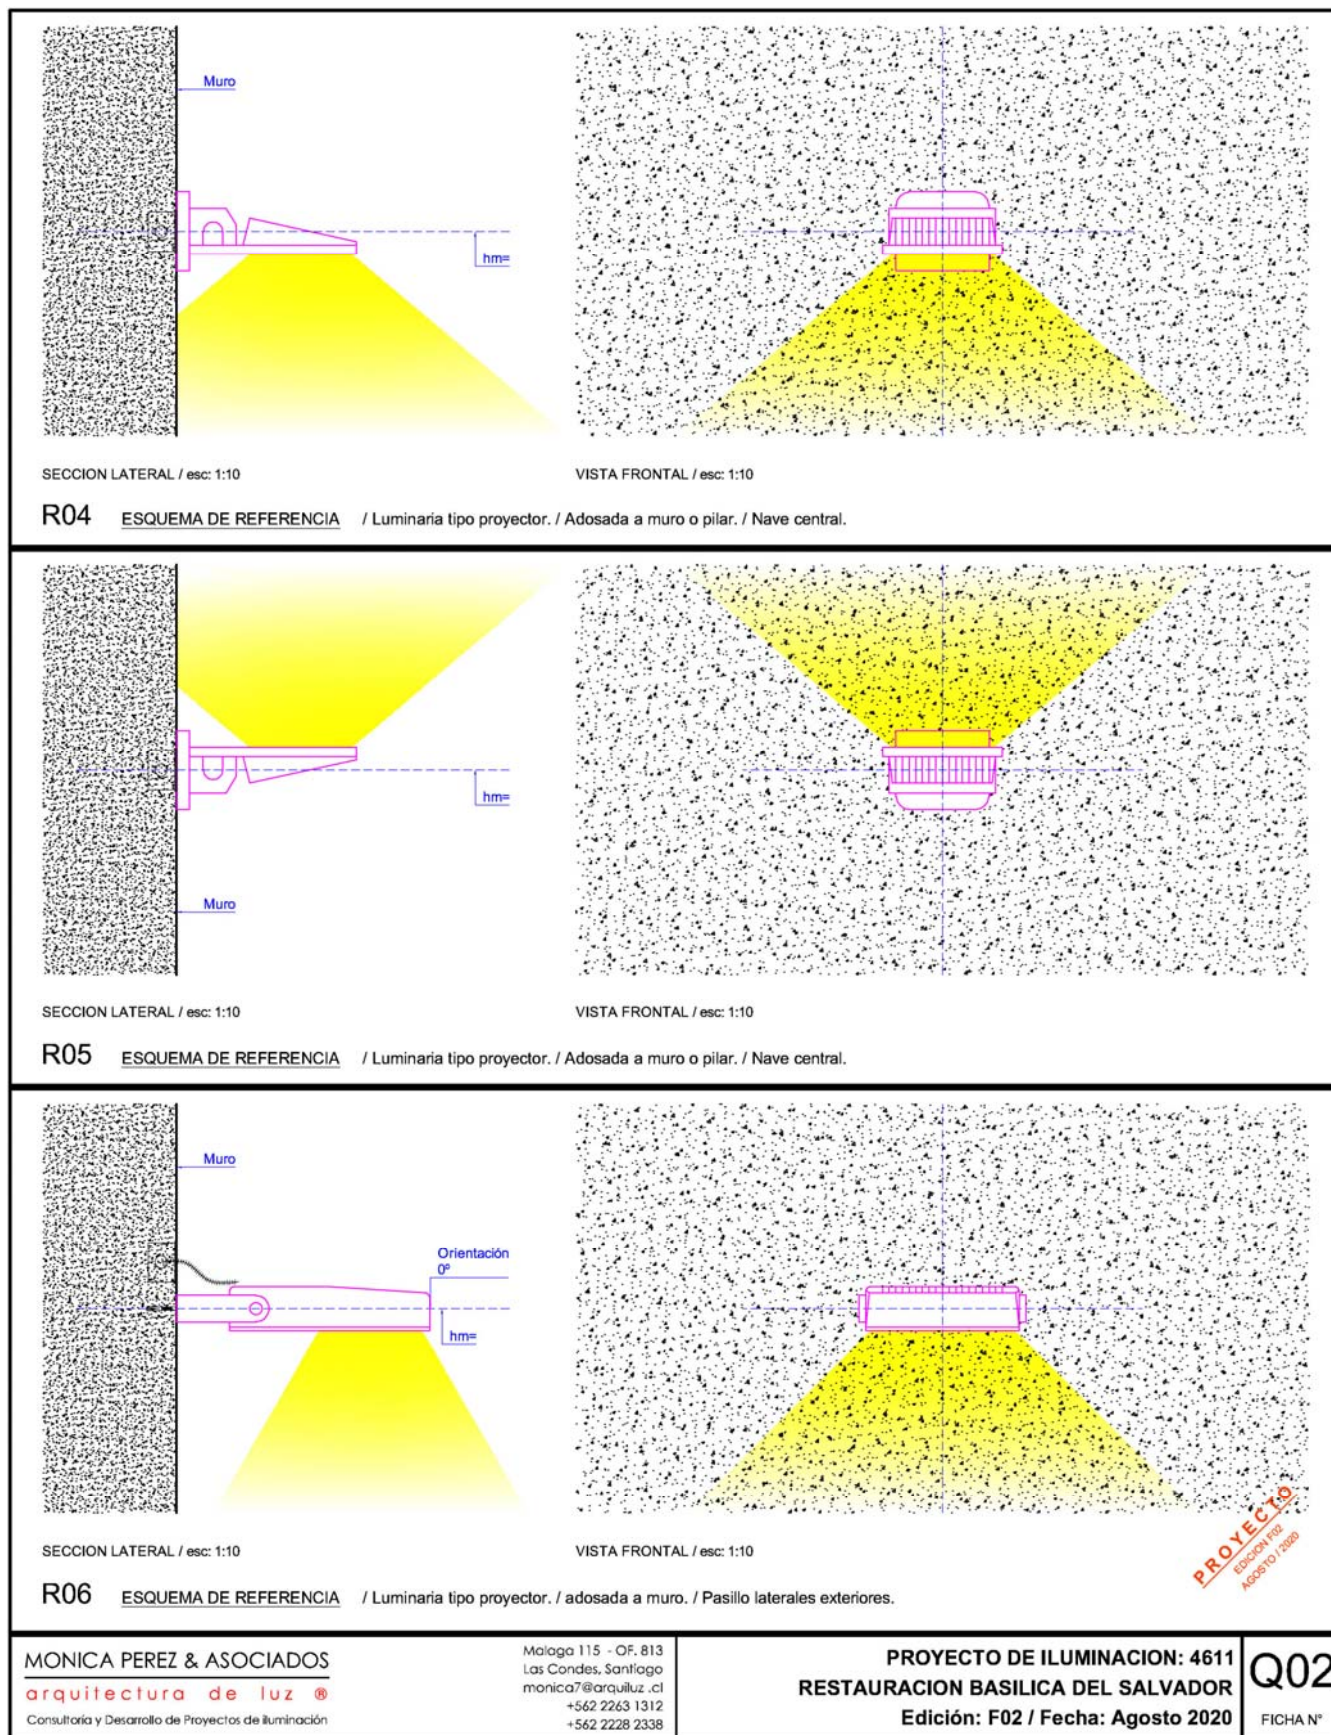

PROYECTO 4611


Fecha

14/08/2020


RESTAURACION BASILICA DEL SALVADOR.

Estado **PROYECTO.**

Edición **E**

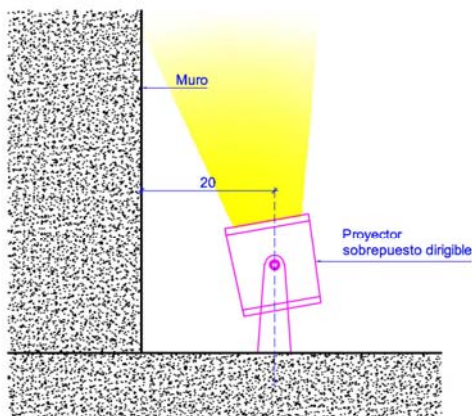


SECCION LATERAL / esc: 1:10

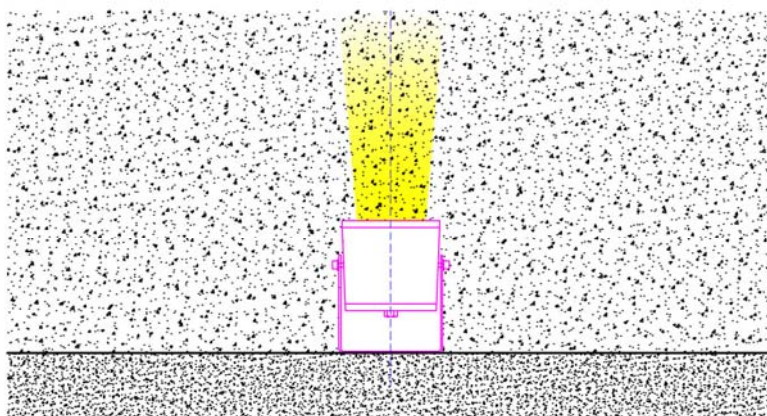


VISTA FRONTAL / esc: 1:10

R07 ESQUEMA DE REFERENCIA / Luminaria spot tipo proyector. / Sobrepujeta en piso o loseta. / Fachadas.

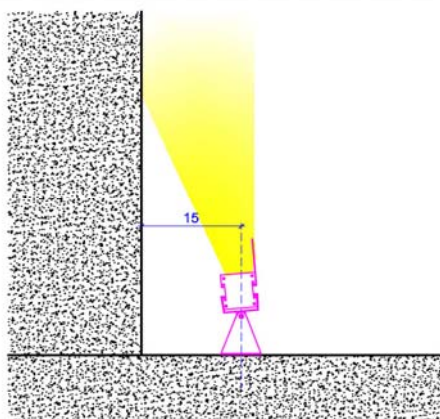


SECCION LATERAL / esc: 1:10

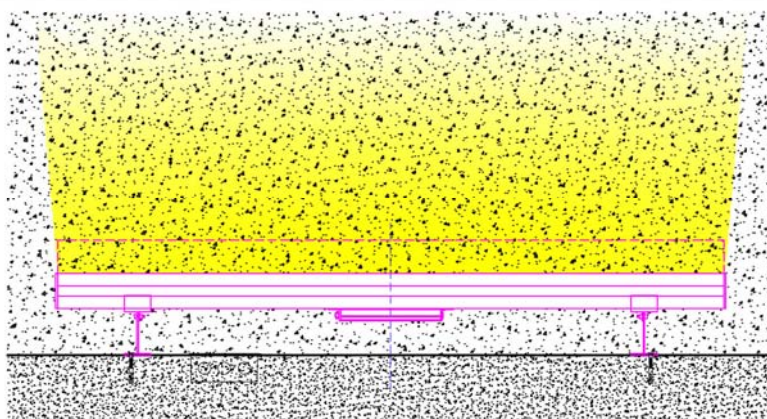


VISTA FRONTAL / esc: 1:10

R08 ESQUEMA DE REFERENCIA / Luminaria tipo proyector lineal. / Sobrepujeta en piso. / Fachada acceso y 2 nivel.

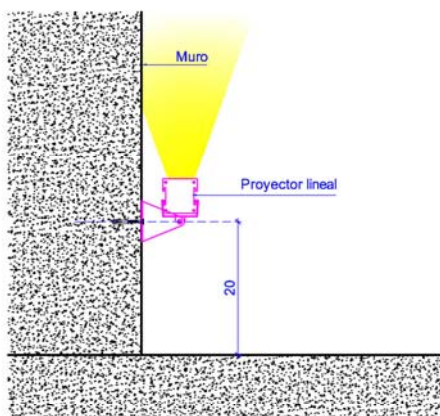

SECCION LATERAL / esc: 1:10

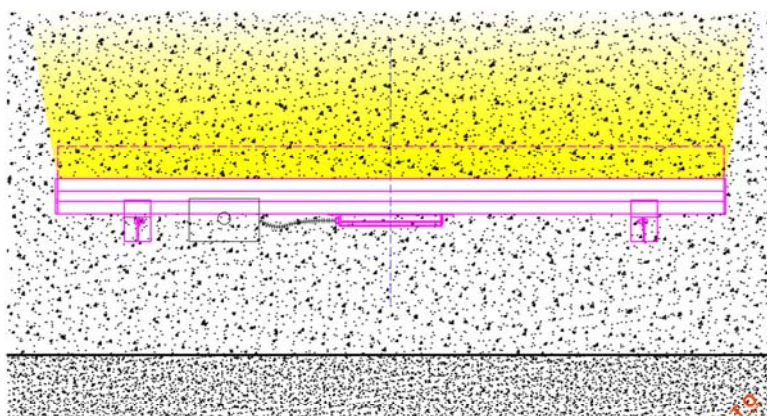

VISTA FRONTAL / esc: 1:10

R09 ESQUEMA DE REFERENCIA / Luminaria tipo proyector lineal. / Adosada a muro. / Fachadas.

PROYECTO
EDICIÓN F02
AGOSTO 2020

MONICA PEREZ & ASOCIADOS
arquitectura de luz ®
Consultoría y Desarrollo de Proyectos de Iluminación

Malaga 115 - OF. 813
Las Condes, Santiago
monica7@arquiluz.cl
+562 2263 1312
+562 2228 2338

PROYECTO DE ILUMINACION: 4611
RESTAURACION BASILICA DEL SALVADOR
Edición: F02 / Fecha: Agosto 2020


Q03
FICHA N°

PROYECTO 4611
RESTAURACION BASILICA DEL SALVADOR.


Estado **PROYECTO.**

Fecha 14/08/2020

Edición **E**

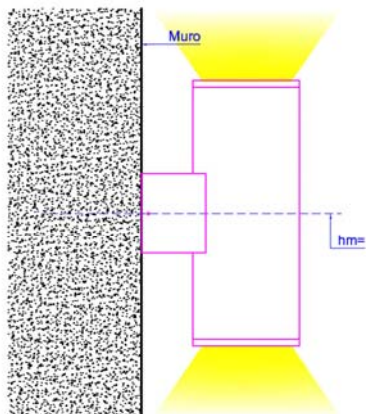


SECCION LATERAL / esc: 1:10

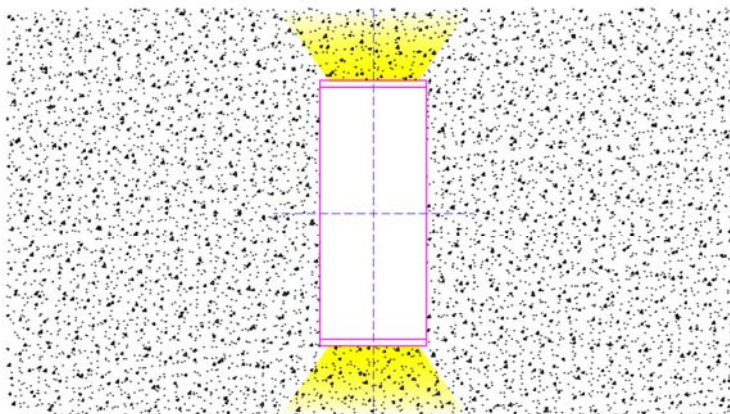


VISTA FRONTAL / esc: 1:10

R10 ESQUEMA DE REFERENCIA / Luminaria hermética, tipo aplique. / adosada a muro. / Fachadas y patio interior.

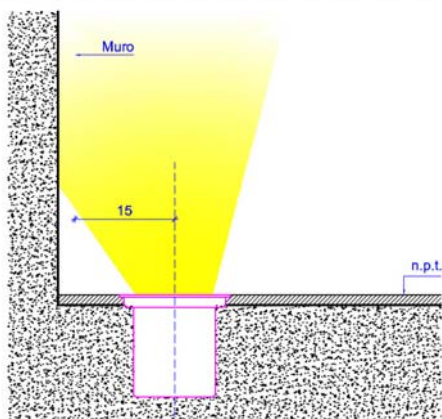


SECCION LATERAL / esc: 1:10

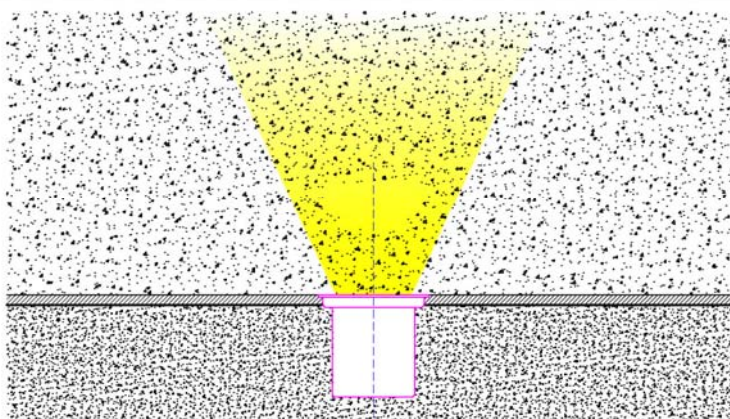


VISTA FRONTAL / esc: 1:10

R11 ESQUEMA DE REFERENCIA / Luminaria spot. / Embutida en piso. / Cripta.

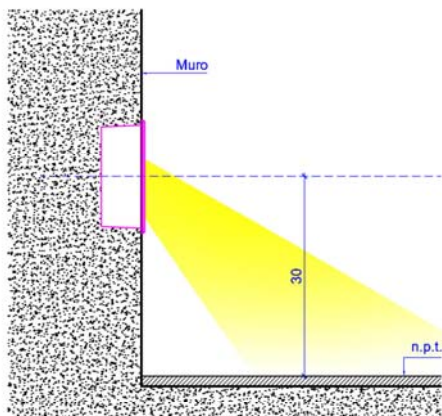

SECCION LATERAL / esc: 1:10

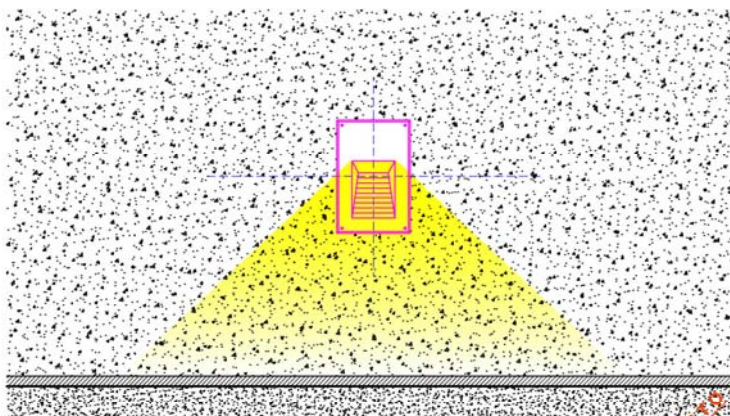

VISTA FRONTAL / esc: 1:10

R12 ESQUEMA DE REFERENCIA / Luminaria de luz rasante. / Embutida en muro. / Escalera acceso cripta.

PROYECTO
EDICION F02
AGOSTO 2020

MONICA PEREZ & ASOCIADOS
arquitectura de luz ®
Consultoría y Desarrollo de Proyectos de Iluminación

Malaga 115 - OF. 813
Las Condes, Santiago
monica7@arquiluz.cl
+562 2263 1312
+562 2228 2338

PROYECTO DE ILUMINACION: 4611
RESTAURACION BASILICA DEL SALVADOR
Edición: F02 / Fecha: Agosto 2020

Q04
FICHA N°

PROYECTO 4611


Fecha

14/08/2020


RESTAURACION BASILICA DEL SALVADOR.

Estado **PROYECTO.**


Edición **E**

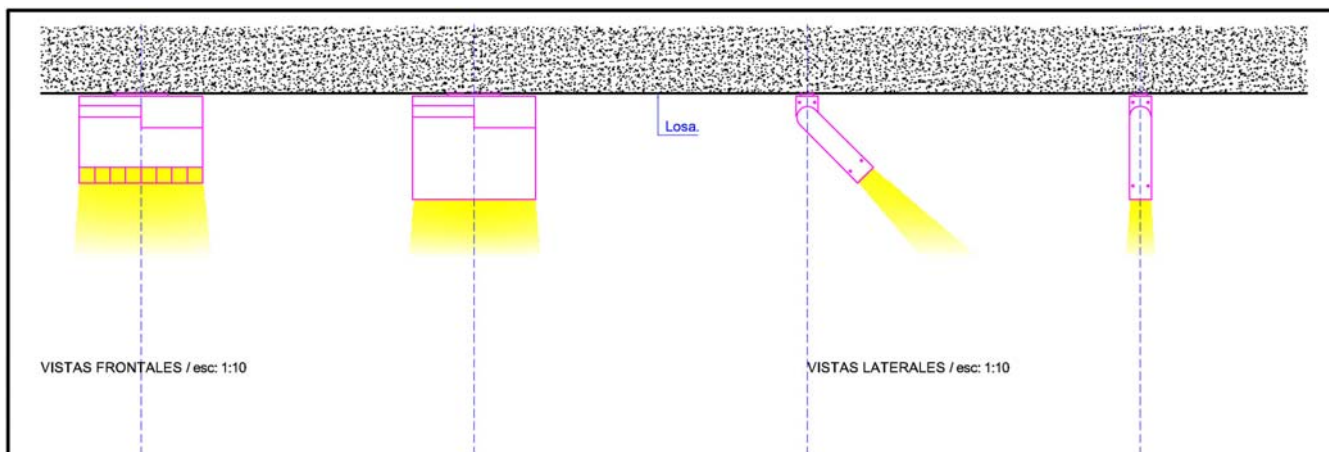

R13 ESQUEMA DE REFERENCIA / Luminaria tipo spot. / Sobrepuesta en losa o cielo. / Cripta.

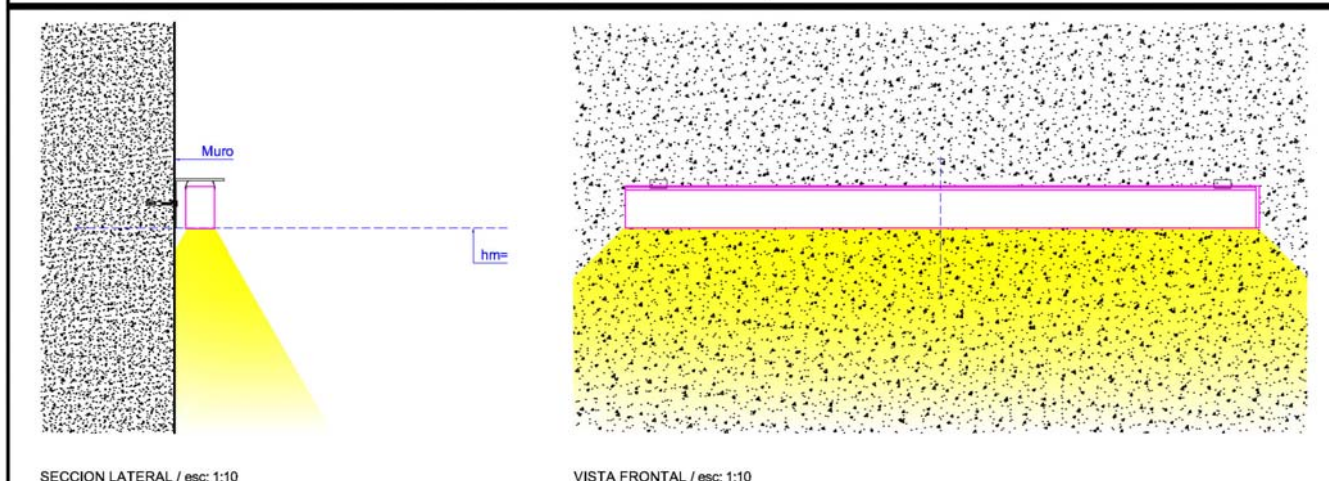

R14 ESQUEMA DE REFERENCIA / Luminaria lineal. / Adosada a muro. / Cripta.

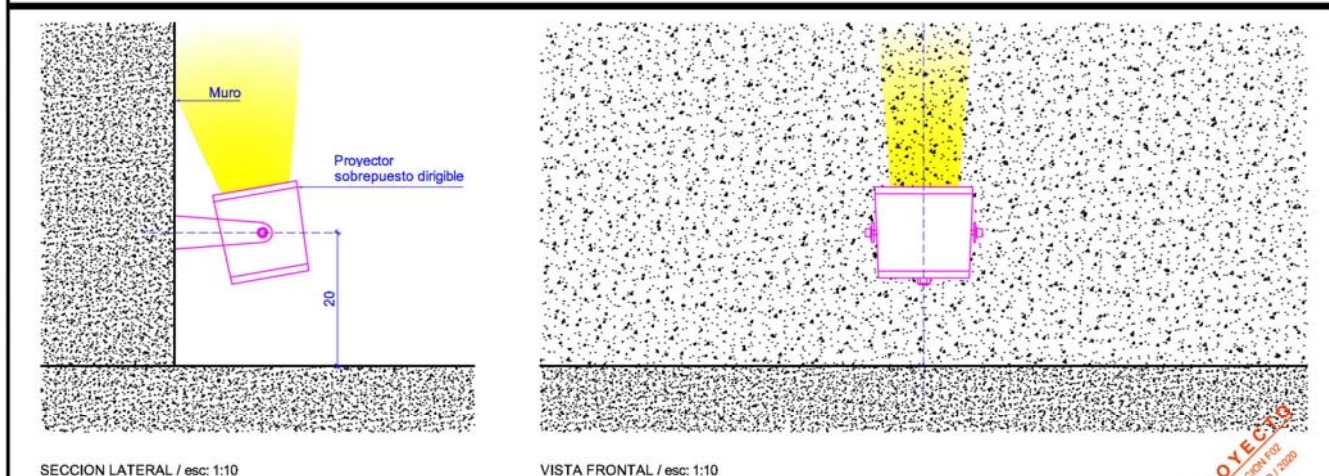

R15 ESQUEMA DE REFERENCIA / Luminaria spot tipo proyector. / Adosado a muro. / Fachadas.

PROYECTO
EDICIÓN F02
AGOSTO 2020

MONICA PEREZ & ASOCIADOS
arquitectura de luz ®
Consultoría y Desarrollo de Proyectos de Iluminación

Málaga 115 - OF. 813
Las Condes, Santiago
monica7@arquiluz.cl
+562 2263 1312
+562 2228 2338

PROYECTO DE ILUMINACION: 4611
RESTAURACION BASILICA DEL SALVADOR
Edición: F02 / Fecha: Agosto 2020

Q05
FICHA Nº

Mónica Pérez & Asociados
14 de Agosto de 2020